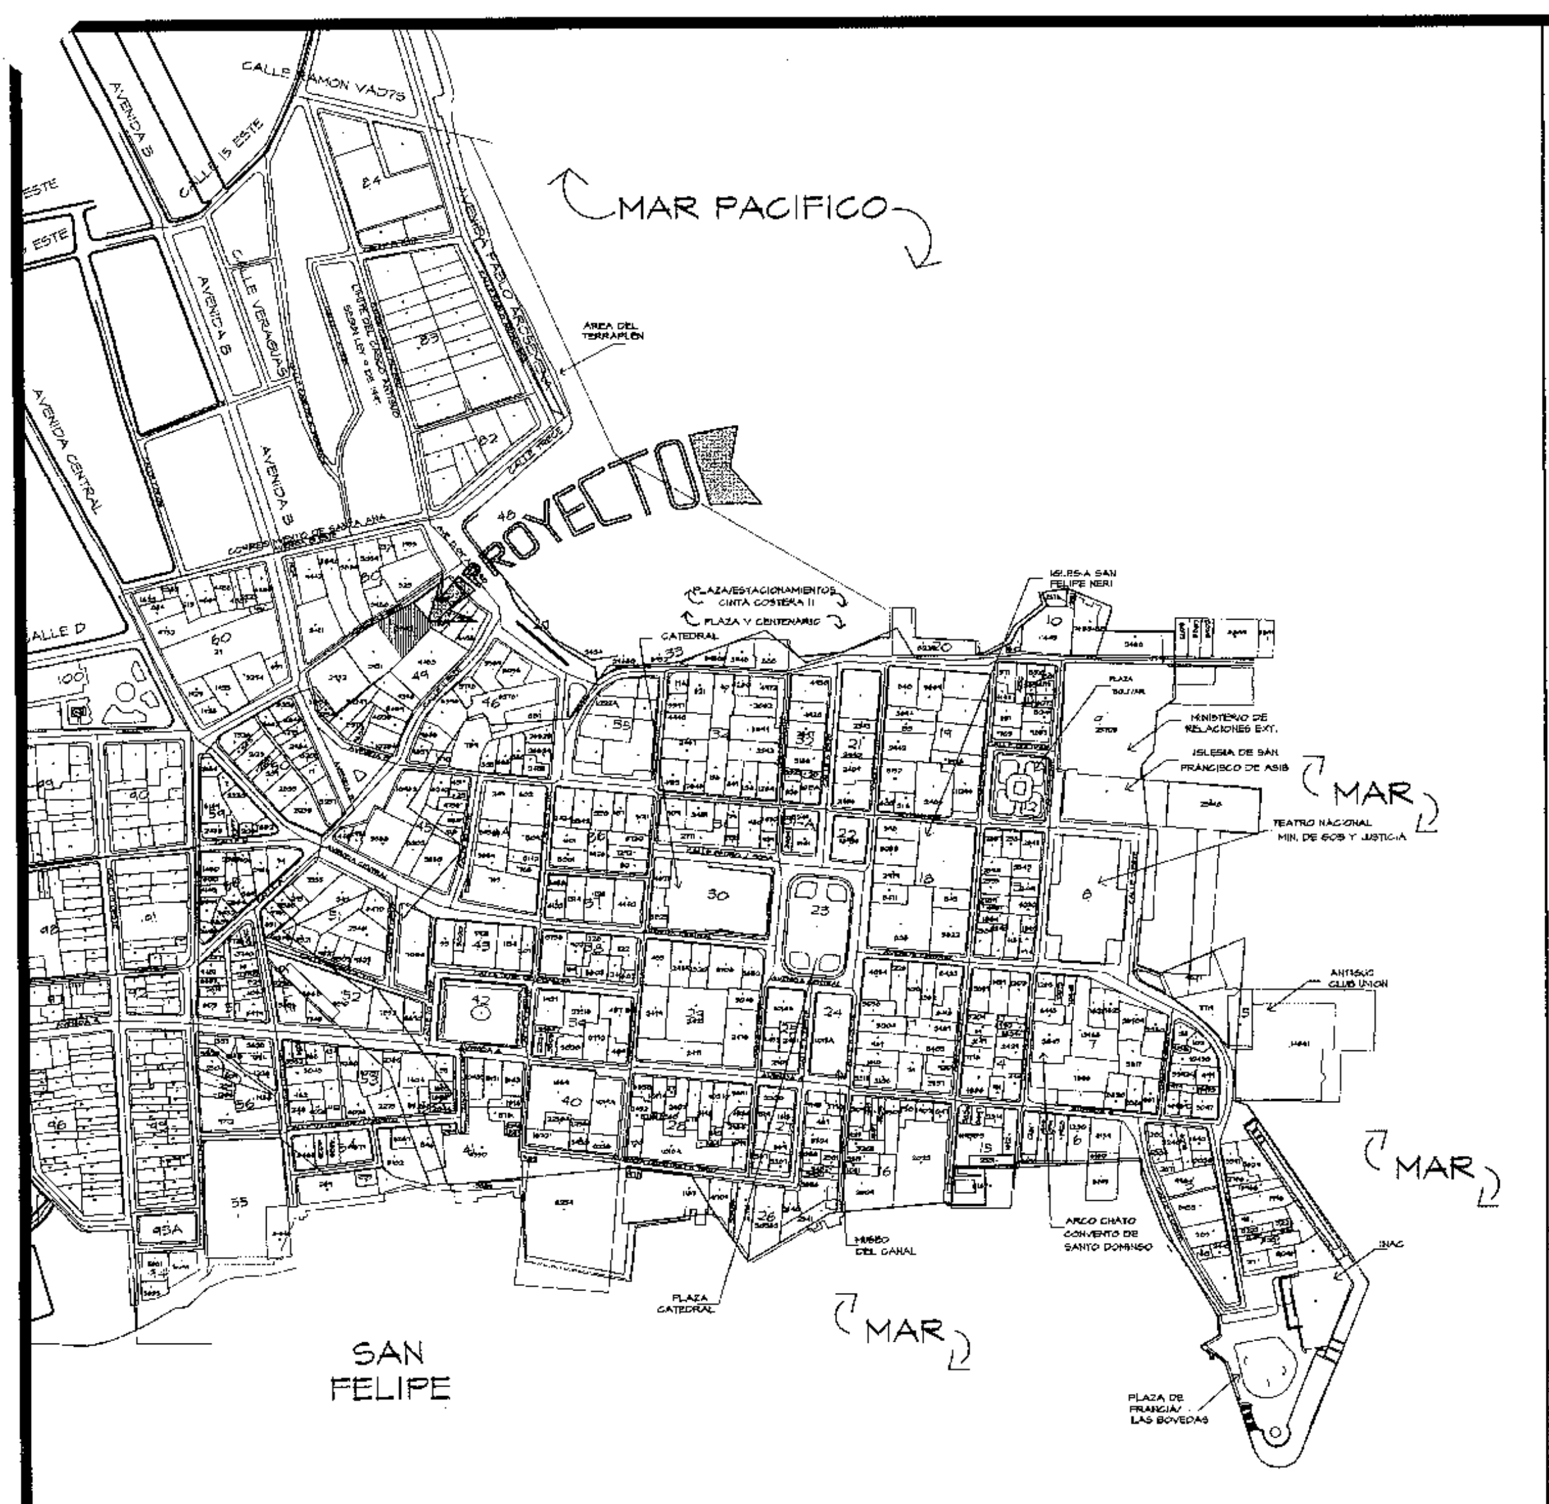

LOCALIZACION REGIONAL
ANTEPROYECTO ESC. 1:5000

NOTAS GENERALES

1. EL PROYECTO COMPRENDE LA REHABILITACIÓN Y PUESTA EN VALOR, INTEGRAL Y DE UN EDIFICIO EXISTENTE DE 3er ORDEN PATRIMONIAL DENTRO DEL CONJUNTO MONUMENTAL HISTÓRICO DEL CASCO ANTIGUO DE LA CIUDAD DE PANAMA.
2. SE PRESERVAN TODOS LOS MUROS DE CALICANTO DE FACHADA, INTERNO Y PERIMETRALES. SE RESTAURARÁ ÍNTEGRAMENTE LA FACHADA FRONTAL, ELIMINANDO TODOS LOS ELEMENTOS DISCORDANTES ACTUALES Y RESALTANDO SU SIGNIFICACIÓN HISTÓRICA.
3. SE MANTIENE LA AUTENTICIDAD EN EL USO EXISTEENTE, ES DECIR, COMERCIAL EN PLANTA BAJA (3 LOCALES COMERCIALES) Y EL RESIDENCIAL EN NIVELES SUPERIORES (25 APARTAMENTOS EFICIENTES).
4. EL PATIO INTERNO ACTUAL (97.73m2) NO LLEGA A LA PLANTA BAJA, PUESTO QUE ARRANCA DESDE LA LOSA DEL NIV. 100. SE PROPONE LLEVARLO HASTA LA PLANTA BAJA (COMO DEBIERA SER), AJUSTÁNDOLO AL NUEVO DISEÑO, QUEDANDO EN 85.14m2. ADICIONALMENTE, SE INTRODUCE UN 2do PATIO INTERNO, POSTERIOR (PARA BRINDAR ILUMINACIÓN Y VENTILACIÓN NATURAL CRUZADA), CON 64.38m2 DE AREA, TODO LO CUAL BRINDA UN TOTAL DE AREA DE PATIOS DE 149.52m2. ES DECIR, SE INCREMENTA LA ACTUAL SUPERFICIE DE PATIO EN +51.79 m2 Y SE LLEVAN HASTA LA PLANTA BAJA.
5. SE MANTENDRÁ LA VOLUMETRÍA, ESCALA Y ALTURAS EXISTENTES, SIN ALTERACIONES.
6. EL PROYECTO CONTEMPLA 4 TANQUES DE GAS (DE 100 Lbs. c/u), UNICAMENTE PARA LOS LOCALES COMERCIALES DE PLANTA BAJA.
7. TINAQUERA: EL EDIFICIO CONTARÁ CON UNA TINAQUERA PROPIA. EN CUALQUIER CASO, LOS INQUILINOS DEL EDIFICIO Y SU CONSERJE, SE COMPROMETEN A SACAR LOS DESHECHOS, EN EL CONTENEDOR EXTERNO MÁS CERCANO, EN EL HORARIO QUE ESTIPULE LA DIRECCIÓN MUNICIPAL DE ASEO URBANO Y DOMICILIARIO (DIMAUD).

RESUMEN DE AREAS

AREA DE LA PARCELA:	733.14 M2
AREA CERRADA TOTAL:	1,668.12 M2
AREA ABIERTA TOTAL:	650.74 M2
AREA TOTAL A CONSTRUIR:	2,318.86 M2

LEYENDA

▭	PAREDES DE BLOQ'S DE CONCRETO DE 4" Ó6" Y REPELLO LISO + PINTURA
----	PROYECCION DE VIGAS DE LOSAS EXISTENTES A RESTAURAR
⬚	EDIFICACION EXISTENTES A MANTENER SIN CAMBIOS
■	COLUMNA NUEVAS A CONSTRUIR
▨	PAREDES, PISOS Y ESTRUCTURAS EXISTENTES A MANTENER Y RESTAURAR.
////	EDIFICIO VECINO ADOSADO.
⬚	LOSA DE CONCRETO NUEVAS
⬚	MURO DE CALICANTO EXIST. A MANTENER/RESTAURAR
(#)	VÉRTICE DEL POLÍGONO DEL TERRENO

DATOS DE LA FINCA

PARCELA:

FINCA: 13362; COD. UBICACION: 8701; TOMO:370 FOLIO: 426,

AREA: 733.14M2

PROPIEDAD DE:

CREATIVE DEVELOPMENT INC.

ZONIFICACION: RM-H2 + C1 (RESIDENCIAL MULTIFAMILIAR DE ALTA DENSIDAD + COMERCIO VECINAL)

CATEGORIA:
"TERCER ORDEN": AQUELLA CON POCO VALOR HISTÓRICO PERO MUCHO VALOR AMBIENTAL

CALCULO DE DENSIDAD:

DENSIDAD PROPUESTA:
USO DE SUELO: RMH2 (1,500 PER/Ha + 20% TOLERANCIA)
DENSIDAD PERMITIDA: 0.0733314Ha X 1,500 PER/Ha (+ 20% TOLERANCIA)= 110 PER (+ 20% TOLERANCIA)
DENSIDAD PROPUESTA:

- APTOS #1, 2, 3, 4, 5, 6, 7, 8, 16, 19, 25= 11 APTOS (2 RECS. C/U) X 2.5 PER C/U= 27.5 PER.
- APTOS #9, 10, 11, 12, 13, 14, 15, 20, 21, 22, 23, 24= 12 APTOS (1 REC. C/U) X 1.5 PER C/U= 18 PER.
- APTOS #17, 28= 2 APTOS (3 RECS. C/U) X 3.5 PER C/U= 7 PER.

TOTAL DENSIDAD PROPUESTA: 27.5 + 18 +7= 52.50 PER

RESUMEN DE AREA POR NIVELES

	NOMBRE	AREA (M2)	AREA TOTAL (M2)
NIVEL 000	LOCALES		
	Local #1	69.46	69.46
	Local #2	67.06	67.06
	Local #3	45.24	45.24
	APARTAMENTOS		
	Apto. #1	49.85	64.69
	Patio Apto. #1	14.84	
	Apto. #2	64.93	85.41
	Patio Apto. #2	20.48	
	Apto. #3	64.94	85.17
	Patio Apto. #3	20.23	
	Apto. #4	57.95	79.96
	Patio Apto. #4	22.01	
	Area Comun Cerrada	101.69	257.25
	Area Comun Abierta	155.56	
SUBTOTAL CONST.			754.24
NIVEL 100	NOMBRE	AREA (M2)	AREA TOTAL (M2)
	Apto. #5	49.85	57.19
	Balcon Apto. #5	7.34	
	Apto. #6	64.93	71.18
	Balcon Apto. #6	6.25	
	Apto. #7	64.94	71.19
	Balcon Apto. #7	6.25	
	Apto. #8	57.95	61.95
	Balcon Apto. #8	4.00	
	Apto. #9	34.08	44.04
	Balcon Apto. #9	9.96	
	Apto. #10	33.74	38.03
	Balcon Apto. #10	4.29	
	Apto. #11	33.77	38.06
	Balcon Apto. #11	4.29	
	Apto. #12	33.72	38.01
	Balcon Apto. #12	4.29	
	Apto. #13	33.69	37.98
	Balcon Apto. #13	4.29	
	Apto. #14	33.73	38.02
	Balcon Apto. #14	4.29	
	Apto. #15	49.48	55.81
	Balcon Apto. #15	6.33	
	Area Comun Cerrada	25.07	95.55
	Area Comun Abierta	70.48	
SUBTOTAL CONST.			647.01
NIVEL 200 y 250	NOMBRE	AREA (M2)	AREA TOTAL (M2)
	Apto. #16	47.69	79.73
	Balcon Apto. #16	3.34	
	Mezzanine Apto.	25.36	
	Balcon Mez Apto.	3.34	
	Apto. #17	64.93	106.52
	Mezzanine Apto.	37.63	
	Balcon Apto. #17	3.96	
	Apto. #18	64.94	106.54
	Mezzanine Apto.	37.64	
	Balcon Apto. #18	3.96	
	Apto. #19	55.80	96.22
	Balcon Apto. #19	3.34	
	Mezzanine Apto.	33.74	
	Balcon Mez Apto.	3.34	
	Apto. #20	34.99	39.39
	Balcon Apto. #20	4.40	
	Apto. #21	32.93	36.85
	Balcon Apto. #21	3.92	
	Apto. #22	33.55	37.84
	Balcon Apto. #22	4.29	
	Apto. #23	34.28	38.86
	Balcon Apto. #23	4.58	
	Apto. #24	32.91	36.94
	Balcon Apto. #24	4.03	
	Apto. #25	70.59	81.17
	Balcon Apto. #25	10.58	
	Area Comun Cerrada	25.07	108.34
	Area Comun Abierta	83.27	
SUBTOTAL CONST.			768.40
NIVEL 300 (AZOTEA)	NOMBRE	AREA (M2)	AREA TOTAL (M2)
	Piso de Equipos 1	22.25	22.25
	Piso de Equipos 2	22.25	22.25
	Piso de Equipos 3	31.52	31.52
	Piso de Equipos 4	21.80	21.80
	Area Comun Abierta	51.39	51.39
SUBTOTAL CONST.			149.21
TOTAL CONST.			AREA TOTAL (M2) 2318.86

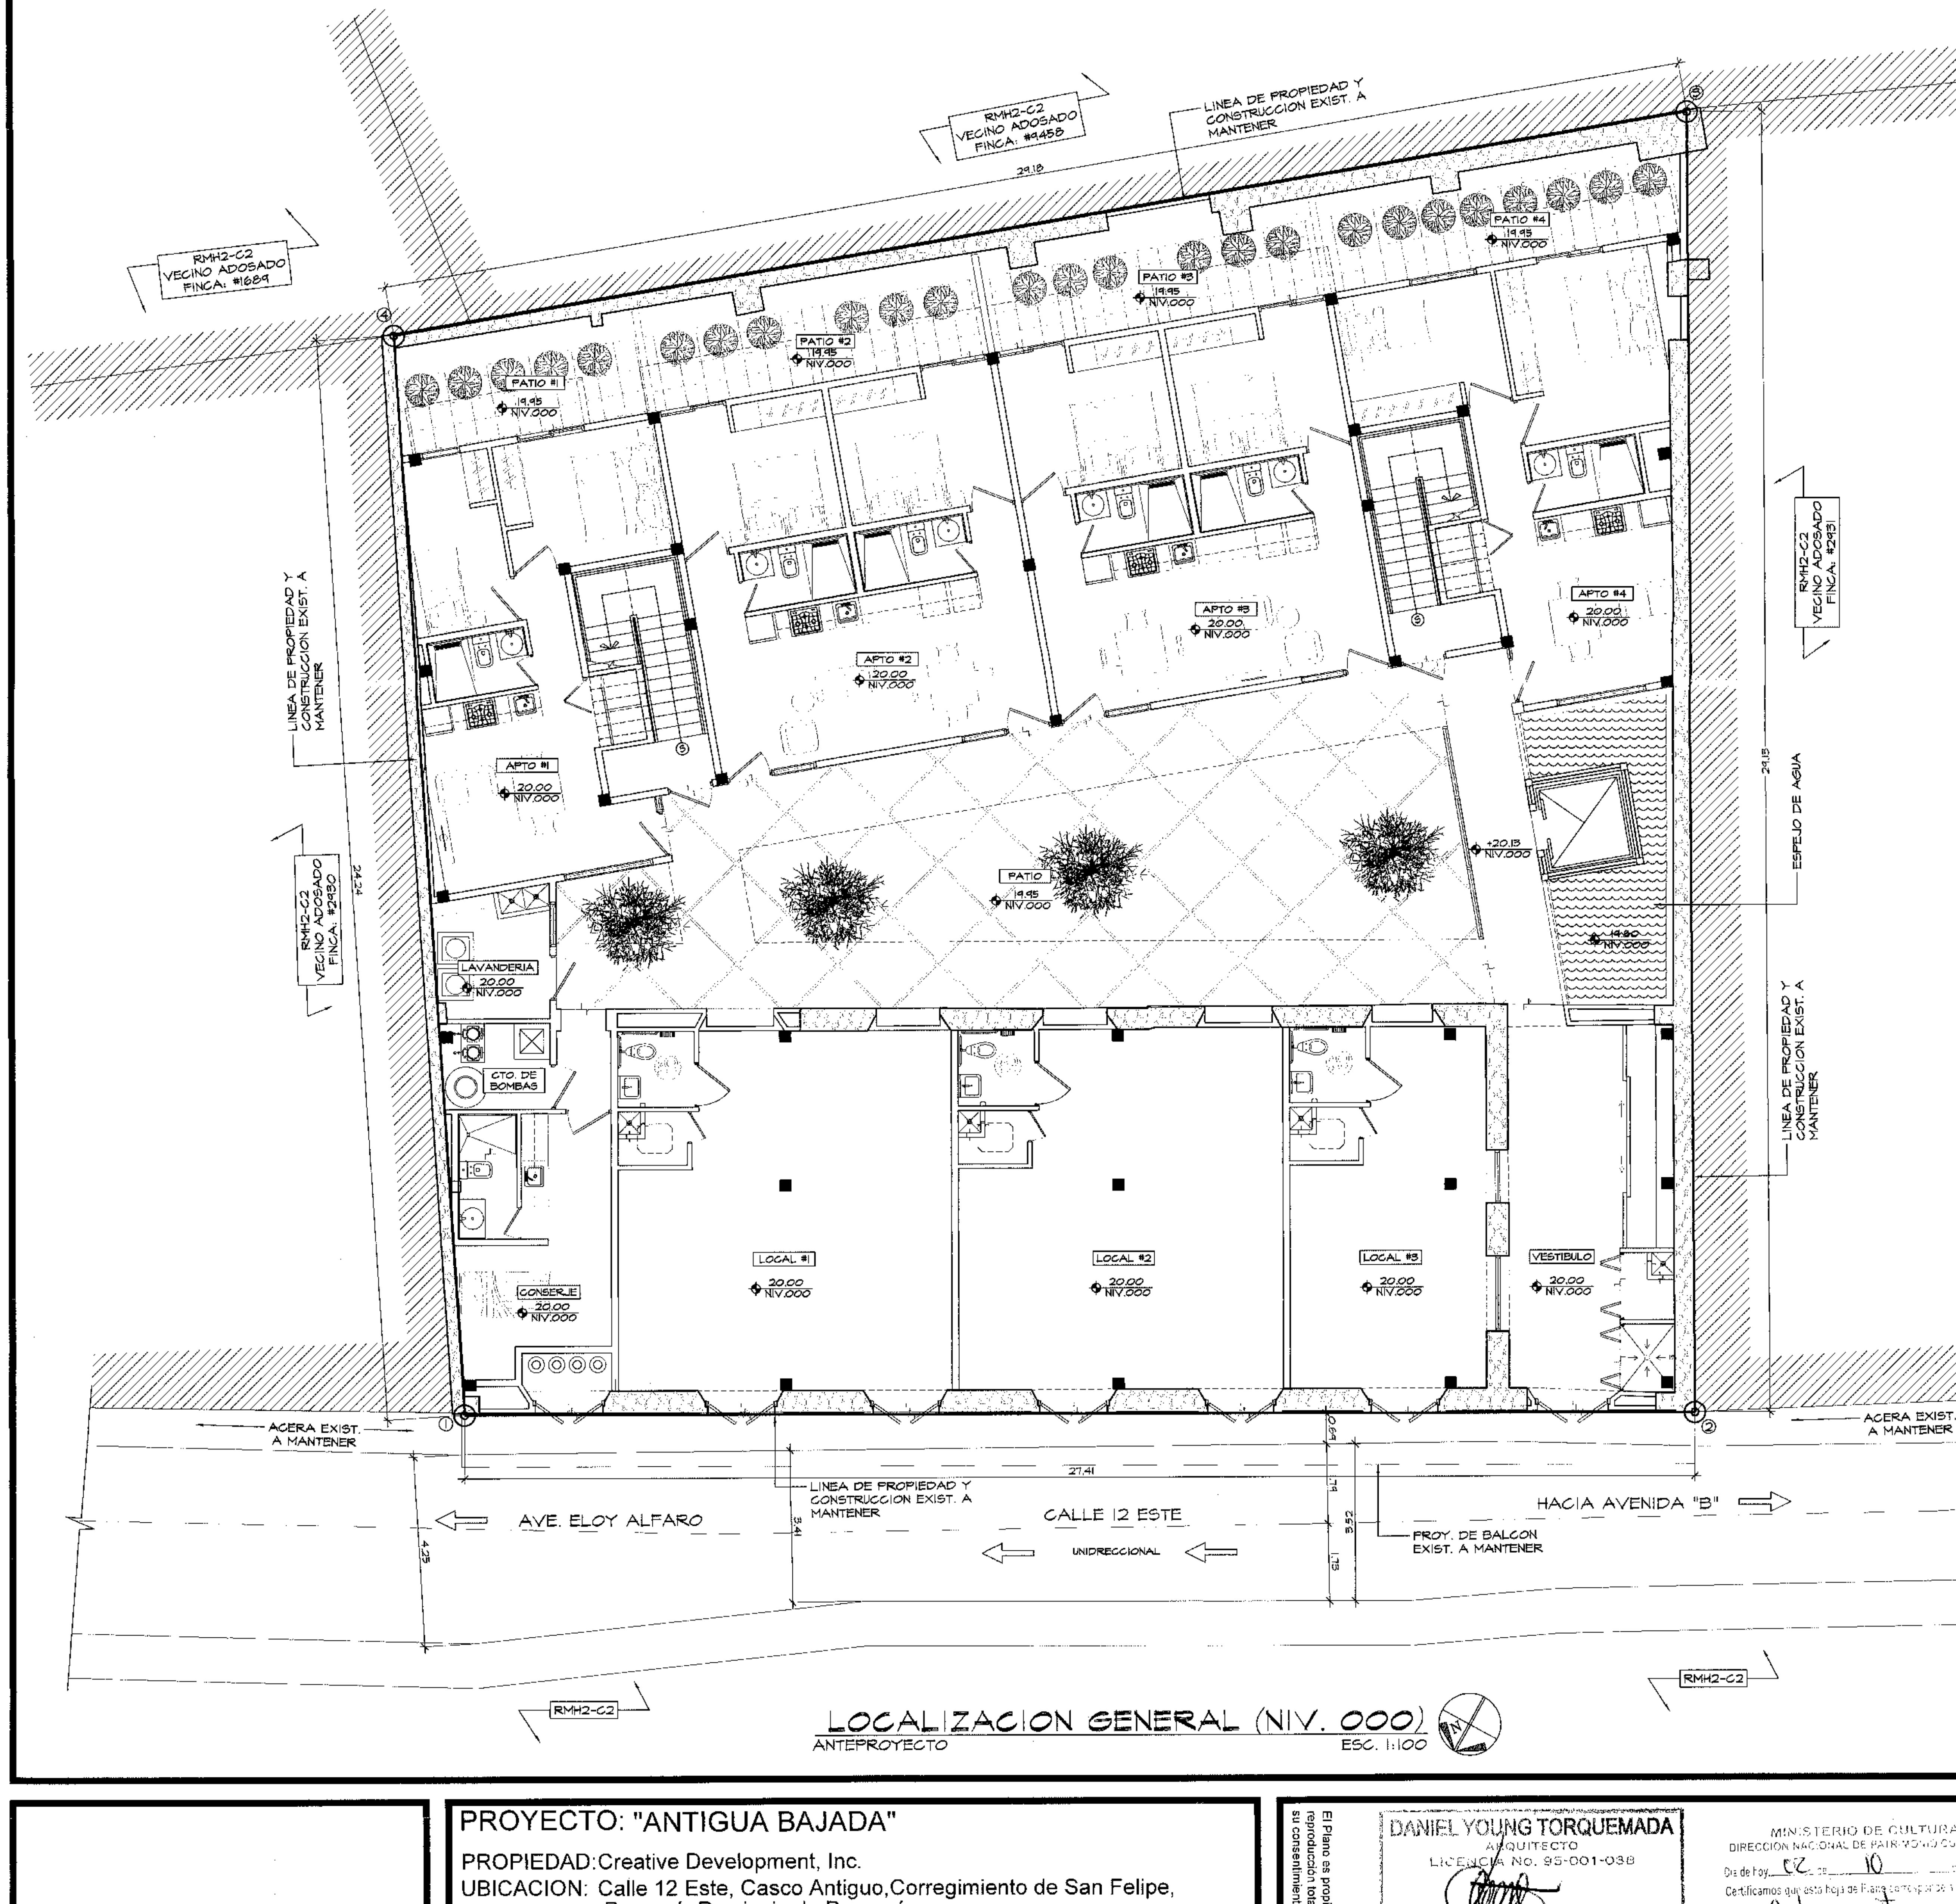

LOCALIZACION GENERAL (NIV. 000)
ANTEPROYECTO ESC. 1:100

YOUNG
TORQUEMADA
ARQUITECTOS

Tel. (507) 264-0711 (507) 264-2670
info@ytarquitectos.com
www.ytarquitectos.com

PROYECTO: "ANTIGUA BAJADA"
PROPIEDAD:Creative Development, Inc.
UBICACION: Calle 12 Este, Casco Antiguo,Corregimiento de San Felipe,
Panamá, Provincia de Panamá

Director de obras y construcciones municipales

Rep. Legal
Céd:2-113-694

DISEÑO:
Arq. Daniel Young Torquemada

DESARROLLO:
Ytarquitectos

DIBUJO:
Ytarquitectos

FECHA
Septiembre 2023

A-01 | 01/11

El Plano es propiedad intelectual del arquitecto esta prohibida su reproducción total o parcial, y no puede ser alterado o modificado sin su consentimiento previo por escrito.

DANIEL YOUNG TORQUEMADA
ARQUITECTO
LICENCIA No. 95-001-038
FIRMA
Ley 15 del 26 de enero de 1959
Junta Técnica de Ingeniería y Arquitectura

MINISTERIO DE CULTURA
DIRECCION NACIONAL DE PATRIMONIO CULTURAL
Dia de hoy 02 de 10 de 23
Certificamos que esta hoja de Plano corresponde a los Planos
Anteproyecto
mediante Resolución No. 160-2023 MC/DNPC
Firma del Director

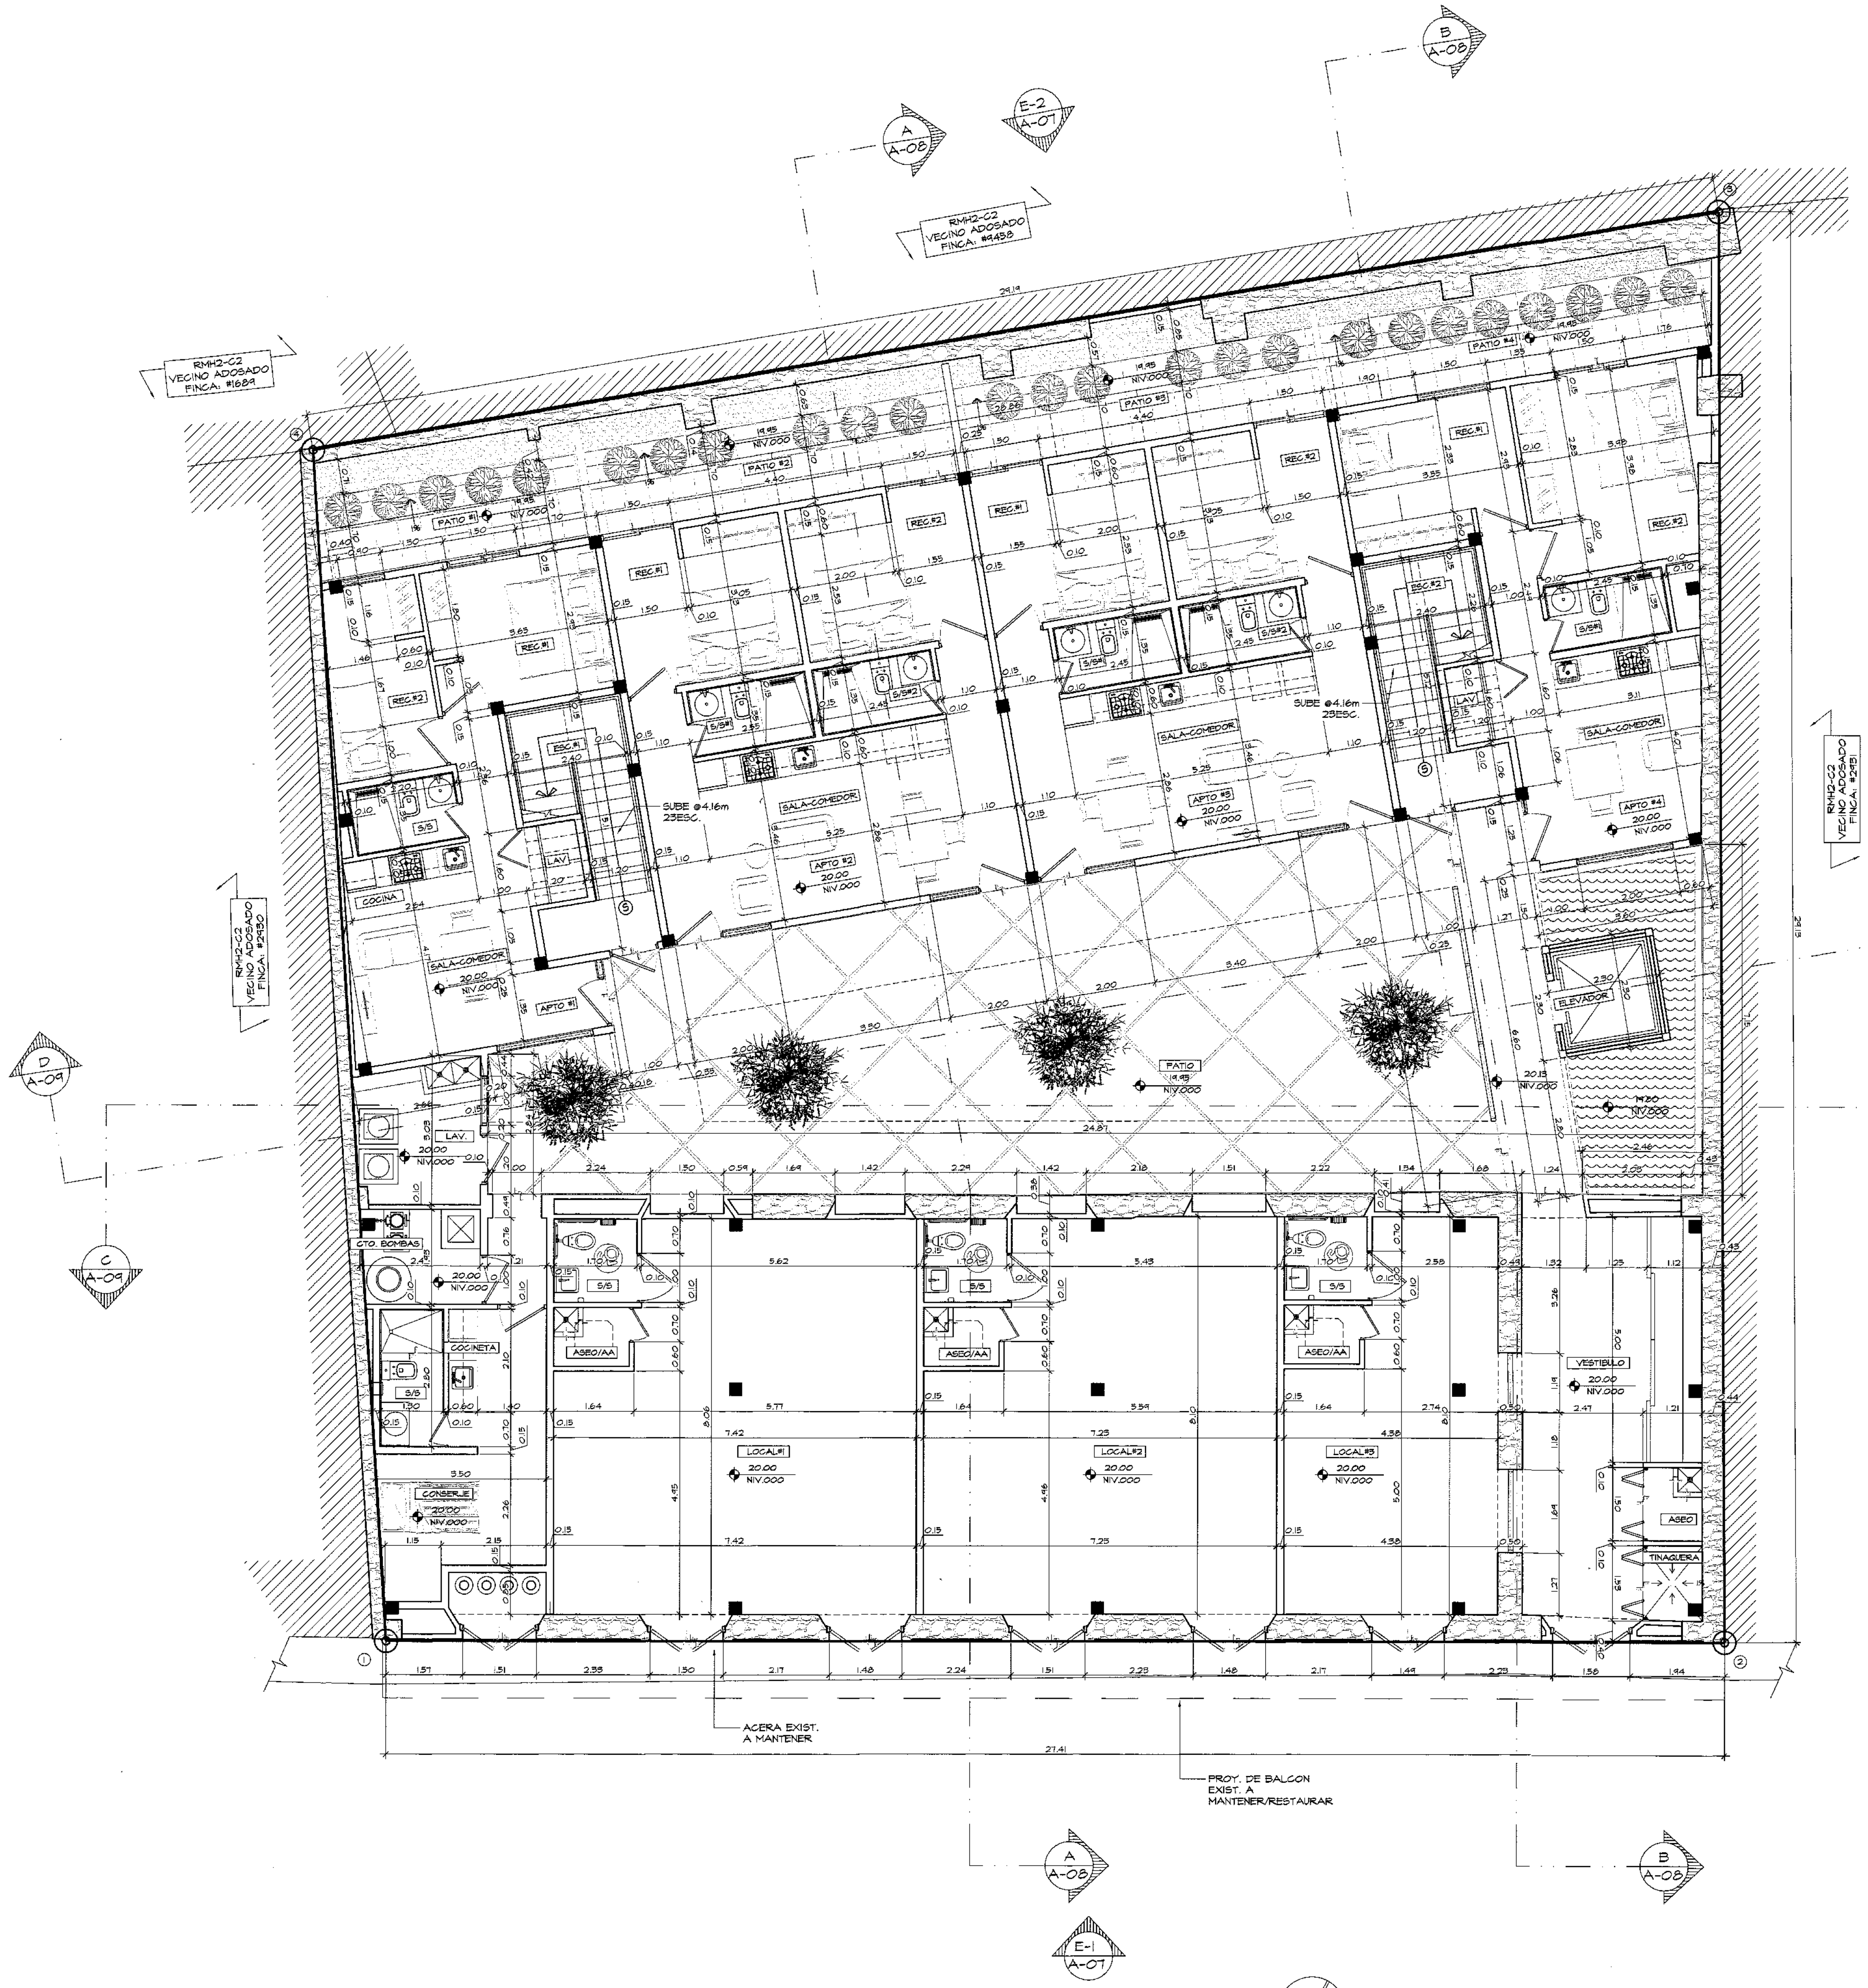

PLANTA ARQUITECTONICA N.000

ANTEPROYECTO

ESC. 1:75

LEYENDA

☐	PAREDES DE BLOQ'S DE CONCRETO DE 4" Ó 6" Y REPELLO LISO + PINTURA	▨	PAREDES, PISOS Y ESTRUCTURAS EXISTENTES A MANTENER Y RESTAURAR.
----	PROYECCION DE VIGAS DE LOSAS EXISTENTES A RESTAURAR	////	EDIFICIO VECINO ADOSADO.
▨	EDIFICACION EXISTENTES A MANTENER SIN CAMBIOS	▒	LOSA DE CONCRETO NUEVAS
■	COLUMNA NUEVAS A CONSTRUIR	▨	MURO DE CALICANTO EXIST. A MANTENER/RESTAURAR
		(#)	VÉRTICE DEL POLÍGONO DEL TERRENO

MINISTERIO DE CULTURA
DIRECCION NACIONAL DE PATRIMONIO CULTURAL
Día de hoy 06 de 10 de 20 23
Certificamos que esta hoja de Plano corresponde a los Planos
Anteproyecto aprobados
mediante Resolución No. 160-2023 MC/DNPC
Firma del Director

DANIEL YOUNG TORQUEMADA
ARQUITECTO
LICENCIA NO. 95-001-038
FIRMA
Ley 15 del 26 de enero de 1959
Junta Técnica de Ingeniería y Arquitectura

El Plano es propiedad intelectual del arquitecto esta prohibida su reproducción total o parcial, y no puede ser alterado o modificado sin su consentimiento previo por escrito.

PROYECTO: "ANTIGUA BAJADA"
PROPIEDAD:Creative Development, Inc.
UBICACION: Calle 12 Este, Casco Antiguo,Corregimiento de San Felipe, Panamá, Provincia de Panamá

Director de obras y construcciones municipales

Rep. Legal
Céd:2-113-694

DISEÑO:
Arq. Daniel Young Torquemada

DESARROLLO:
Ytarquitectos

DIBUJO:
Ytarquitectos

FECHA
Septiembre 2023

A-02 | 02/11

YOUNG
TORQUEMADA
ARQUITECTOS

Tel. (507) 264-0711 (507) 264-2670
info@ytarquitectos.com
www.ytarquitectos.com

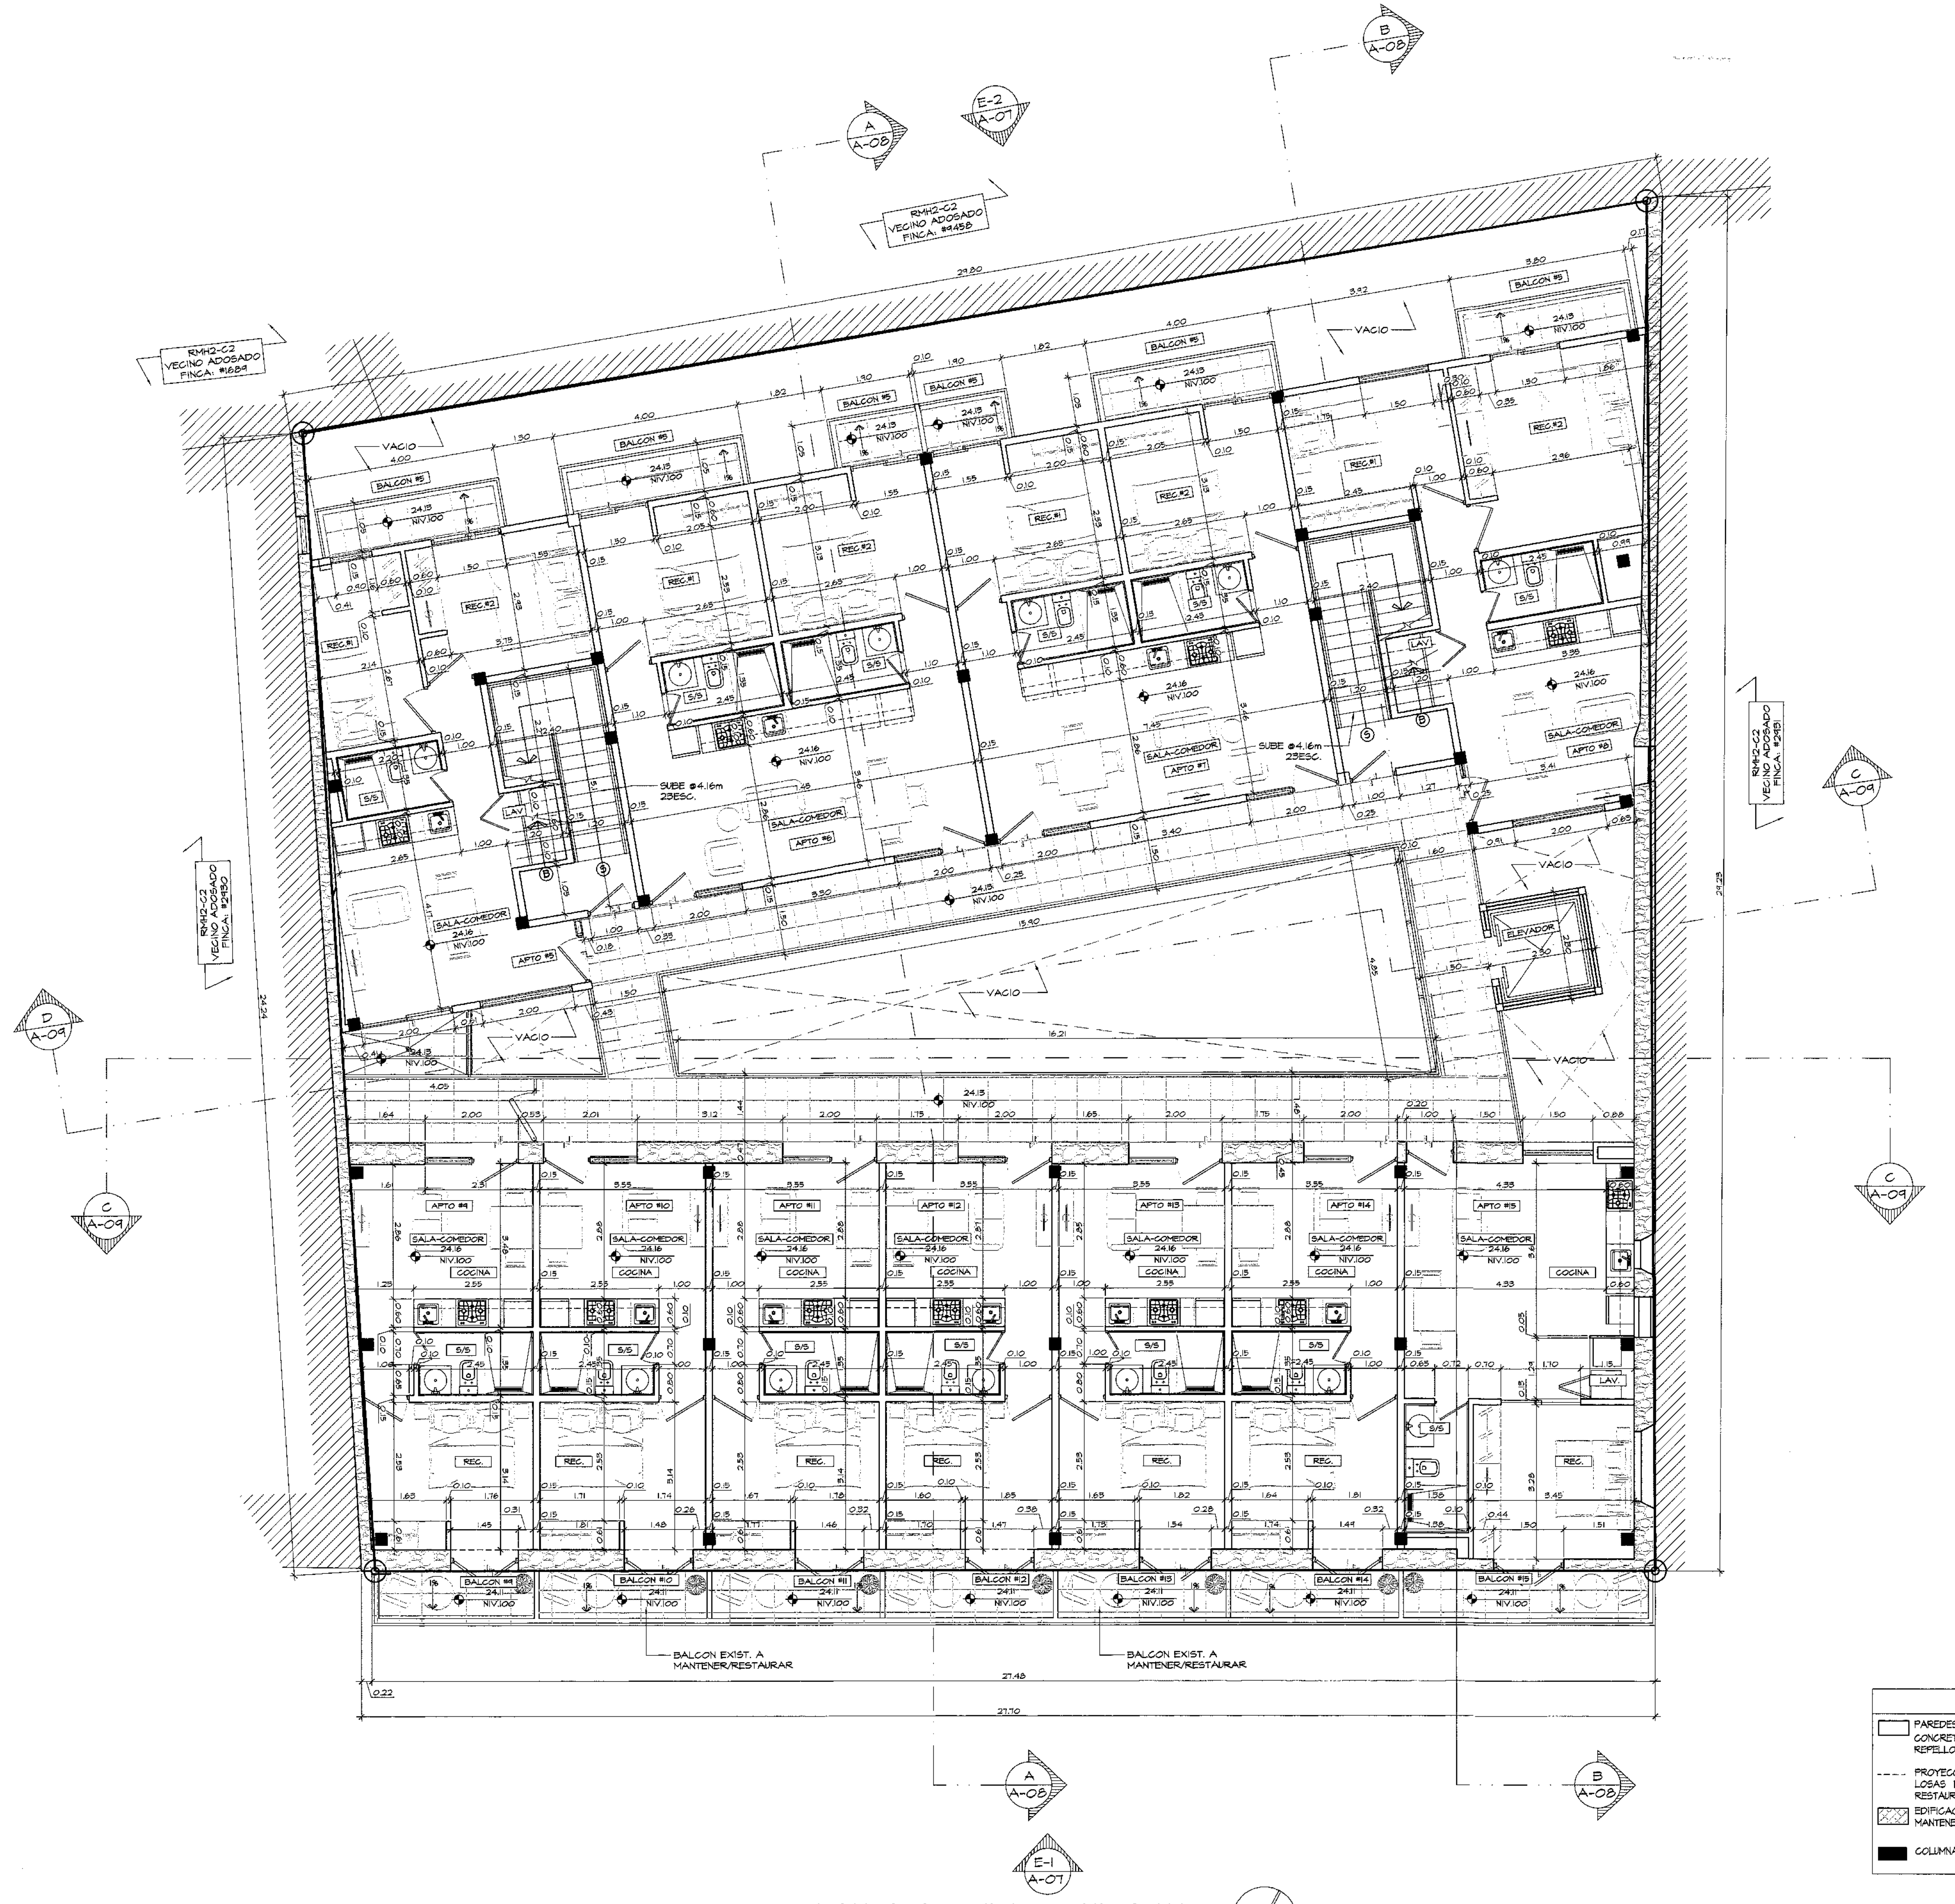

PLANTA ARQUITECTONICA N.100

ANTEPROYECTO

ESC. 1:75

LEYENDA

☐	PAREDES DE BLOQ'S DE CONCRETO DE 4" Ó 6" Y REPELLO LISO + PINTURA
▨	PAREDES, PISOS Y ESTRUCTURAS EXISTENTES A MANTENER Y RESTAURAR.
- - - -	PROYECCION DE VIGAS DE LOSAS EXISTENTES A RESTAURAR
▨	EDIFICIO VECINO ADOSADO.
▨	LOSA DE CONCRETO NUEVAS
▨	EDIFICACION EXISTENTES A MANTENER SIN CAMBIOS
▨	MURO DE CALICANTO EXIST. A MANTENER/RESTAURAR
■	COLUMNA NUEVAS A CONSTRUIR
○	VÉRTICE DEL POLÍGONO DEL TERRENO

MINISTERIO DE CULTURA
DIRECCION NACIONAL DE PATRIMONIO CULTURAL
Dia de hoy 02 de 10 de 2023
Certificamos que esta hoja de Plano corresponde [illegible]
Anteproyecto [illegible]
mediante Resolución N. 160-2023 MC-DNPC
Firma del Director

DANIEL YOUNG TORQUEMADA
ARQUITECTO
LICENCIA No. 95-001-038
FIRMA
Ley 15 del 26 de enero de 1959
Junta Técnica de Ingeniería y Arquitectura

El Plano es propiedad intelectual del arquitecto esta prohibida su reproducción total o parcial, y no puede ser alterado o modificado sin su consentimiento previo por escrito.

PROYECTO: "ANTIGUA BAJADA"

PROPIEDAD: Creative Development, Inc.
UBICACION: Calle 12 Este, Casco Antiguo, Corregimiento de San Felipe,
Panamá, Provincia de Panamá

Director de obras y construcciones municipales

Rep. Legal
Céd:2-113-694

DISEÑO:
Arq. Daniel Young Torquemada

DESARROLLO:
Ytarquitectos

DIBUJO:
Ytarquitectos

FECHA
Septiembre 2023

A-03

03/11

YOUNG
TORQUEMADA
ARQUITECTOS

Tel. (507) 264-0711 (507) 264-2670
info@ytarquitectos.com
www.ytarquitectos.com

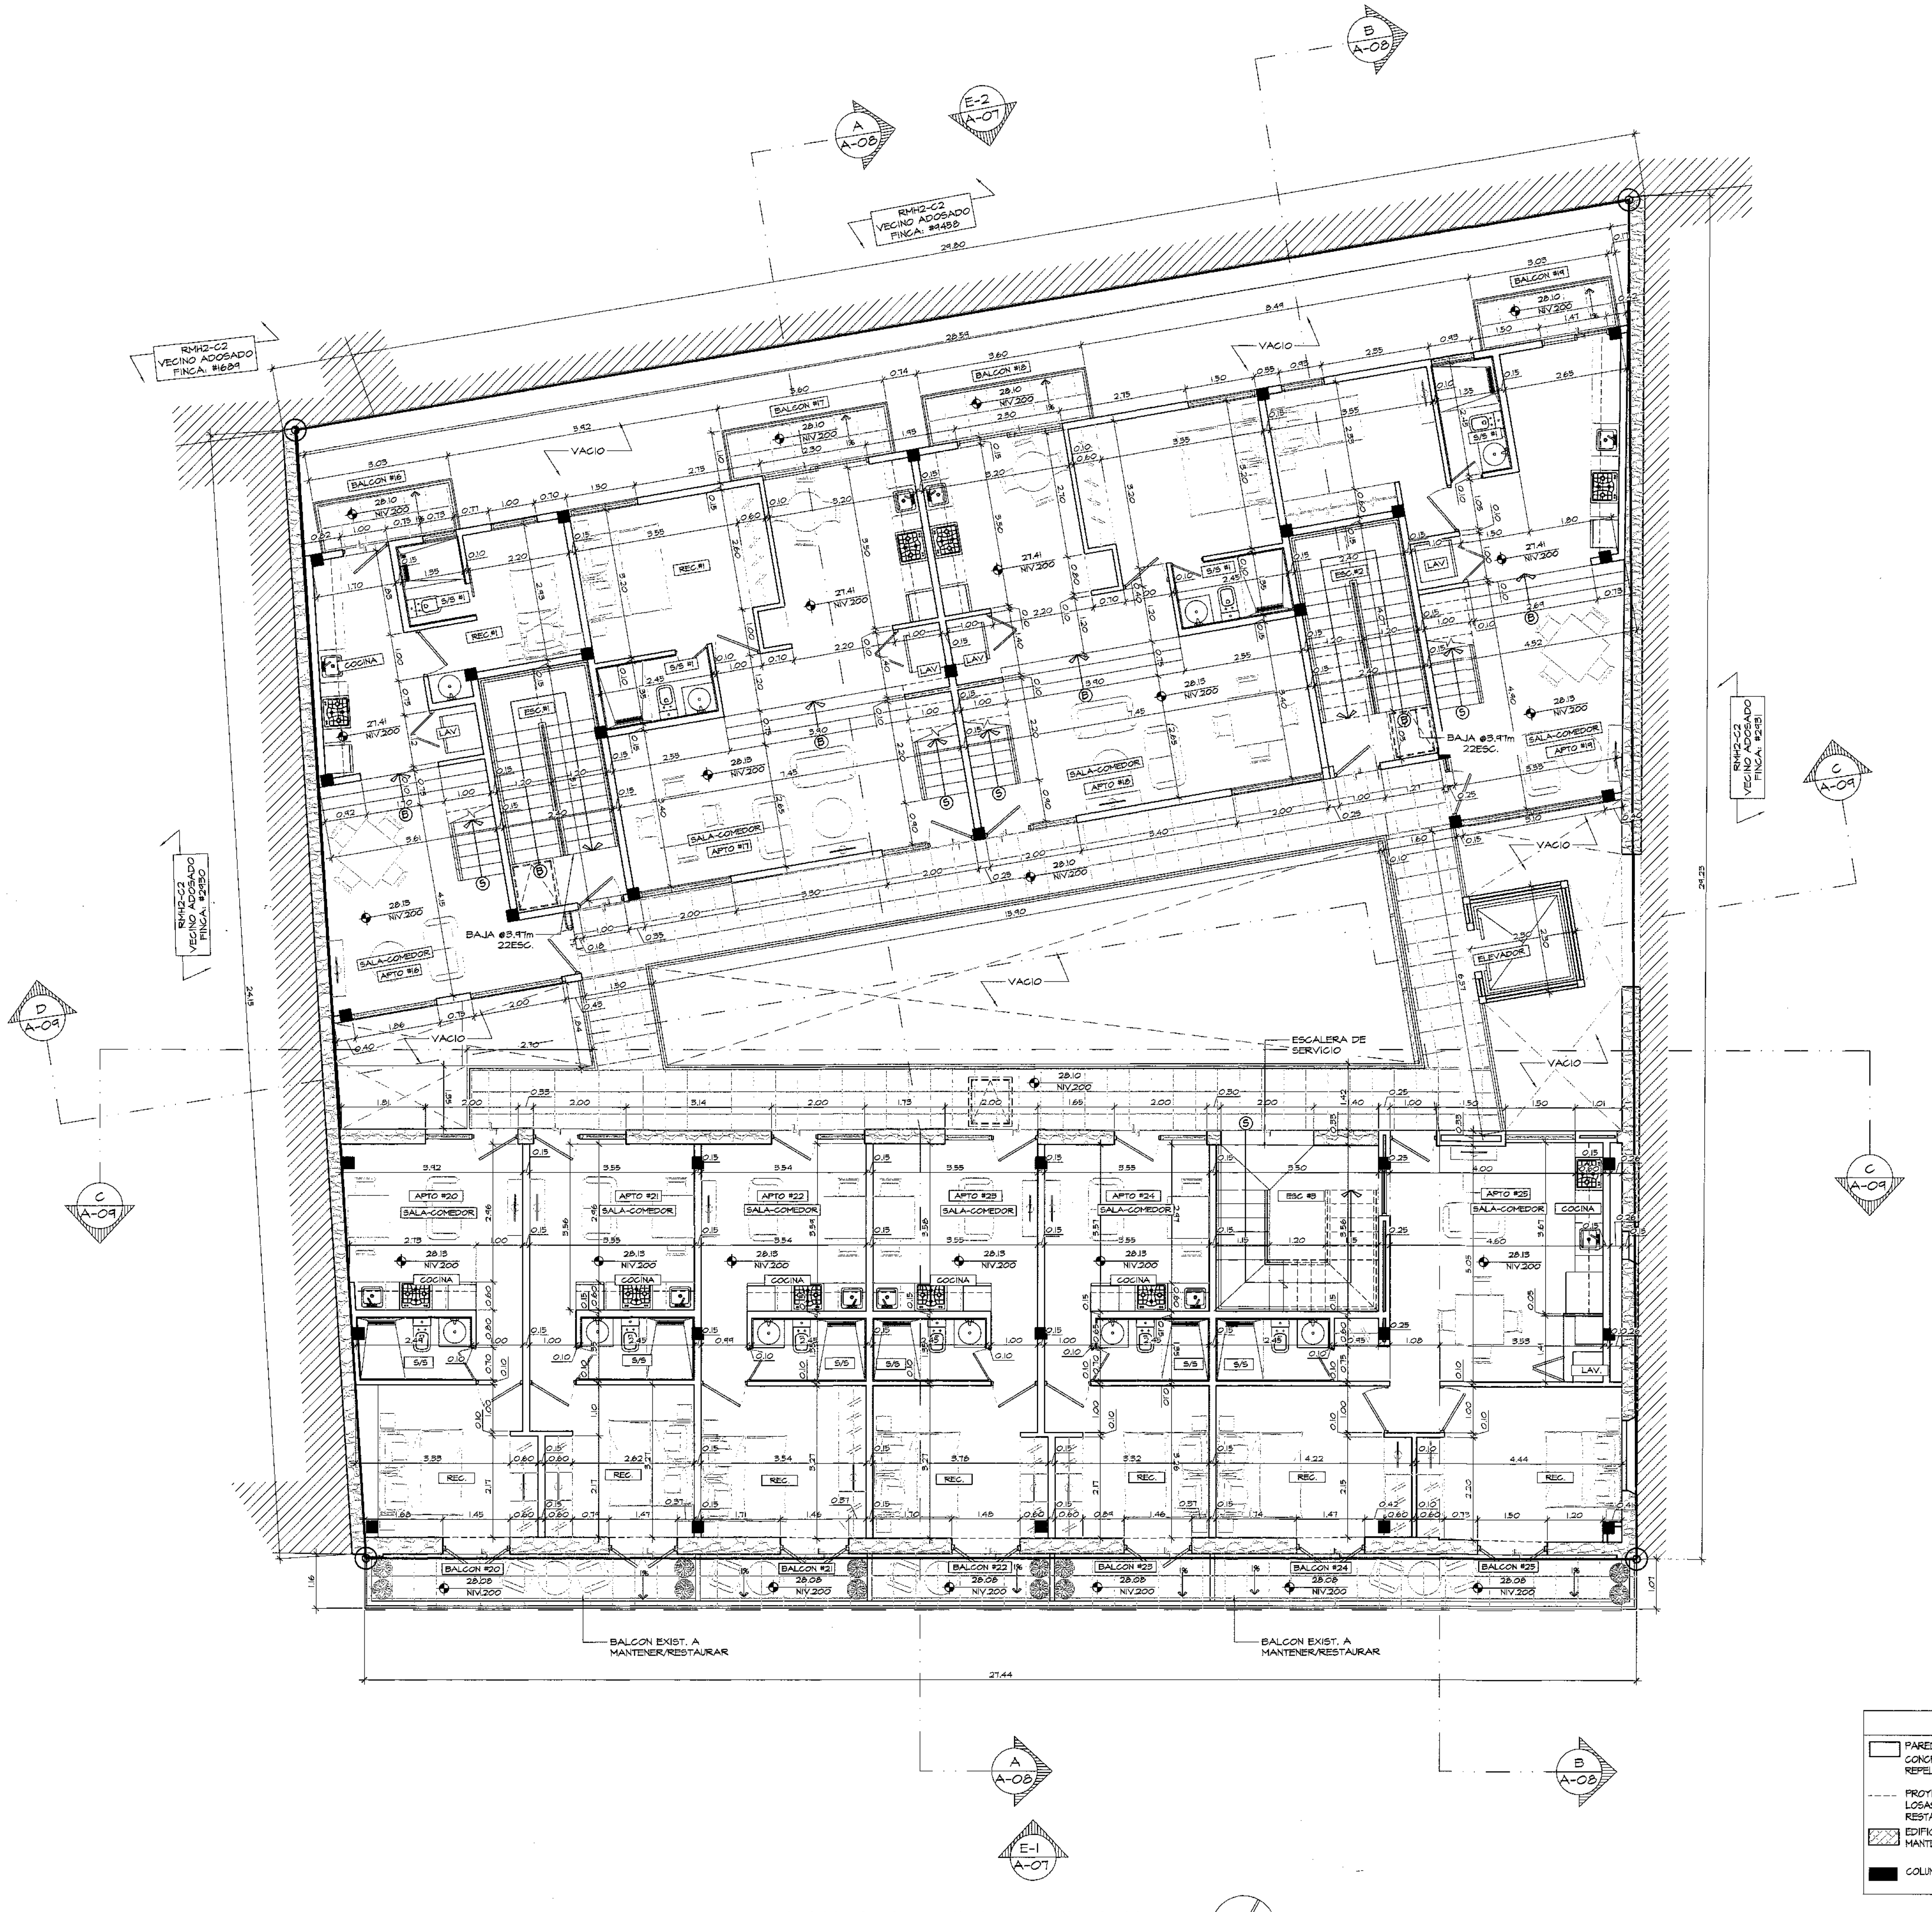

PLANTA ARQUITECTONICA N.200

ANTEPROYECTO
ESC. 1:75

LEYENDA

☐	PAREDES DE BLOQ'S DE CONCRETO DE 4" Ó 6" Y REPELLO LISO + PINTURA	▨	PAREDES, PISOS Y ESTRUCTURAS EXISTENTES A MANTENER Y RESTAURAR.
- - - -	PROYECCION DE VIGAS DE LOSAS EXISTENTES A RESTAURAR	////	EDIFICIO VECINO ADOSADO.
▨	EDIFICACION EXISTENTES A MANTENER SIN CAMBIOS	▨	LOSA DE CONCRETO NUEVAS
■	COLUMNA NUEVAS A CONSTRUIR	▨	MURO DE CALICANTO EXIST. A MANTENER/RESTAURAR
		⊙ #	VÉRTICE DEL POLÍGONO DEL TERRENO

MINISTERIO DE CULTURA
DIRECCION NACIONAL DE PATRIMONIO CULTURAL
Día de hoy 06 de 10 de 20 23
Certificamos que esta hoja de Plano corresponde a los Planos
Anteproyecto aprobados
mediante Resolución No. 160-2023 DNPC
Firma del Director

DANIEL YOUNG TORQUEMADA
ARQUITECTO
LICENCIA No. 85-001-039
FIRMA
Ley 15 del 26 de enero de 1959
Junta Técnica de Ingeniería y Arquitectura

El Plano es propiedad intelectual del arquitecto esta prohibida su reproducción total o parcial, y no puede ser alterado o modificado sin su consentimiento previo por escrito.

PROYECTO: "ANTIGUA BAJADA"
PROPIEDAD:Creative Development, Inc.
UBICACION: Calle 12 Este, Casco Antiguo,Corregimiento de San Felipe, Panamá, Provincia de Panamá

DISEÑO:
Arq. Daniel Young Torquemada

DESARROLLO:
Ytarquitectos

DIBUJO:
Ytarquitectos

FECHA
Septiembre 2023

Director de obras y construcciones municipales

Rep. Legal
Céd:2-113-694

A-04

04 / 11

YOUNG
TORQUEMADA
ARQUITECTOS
Tel. (507) 264-0711 (507) 264-2670
info@ytarquitectos.com
www.ytarquitectos.com

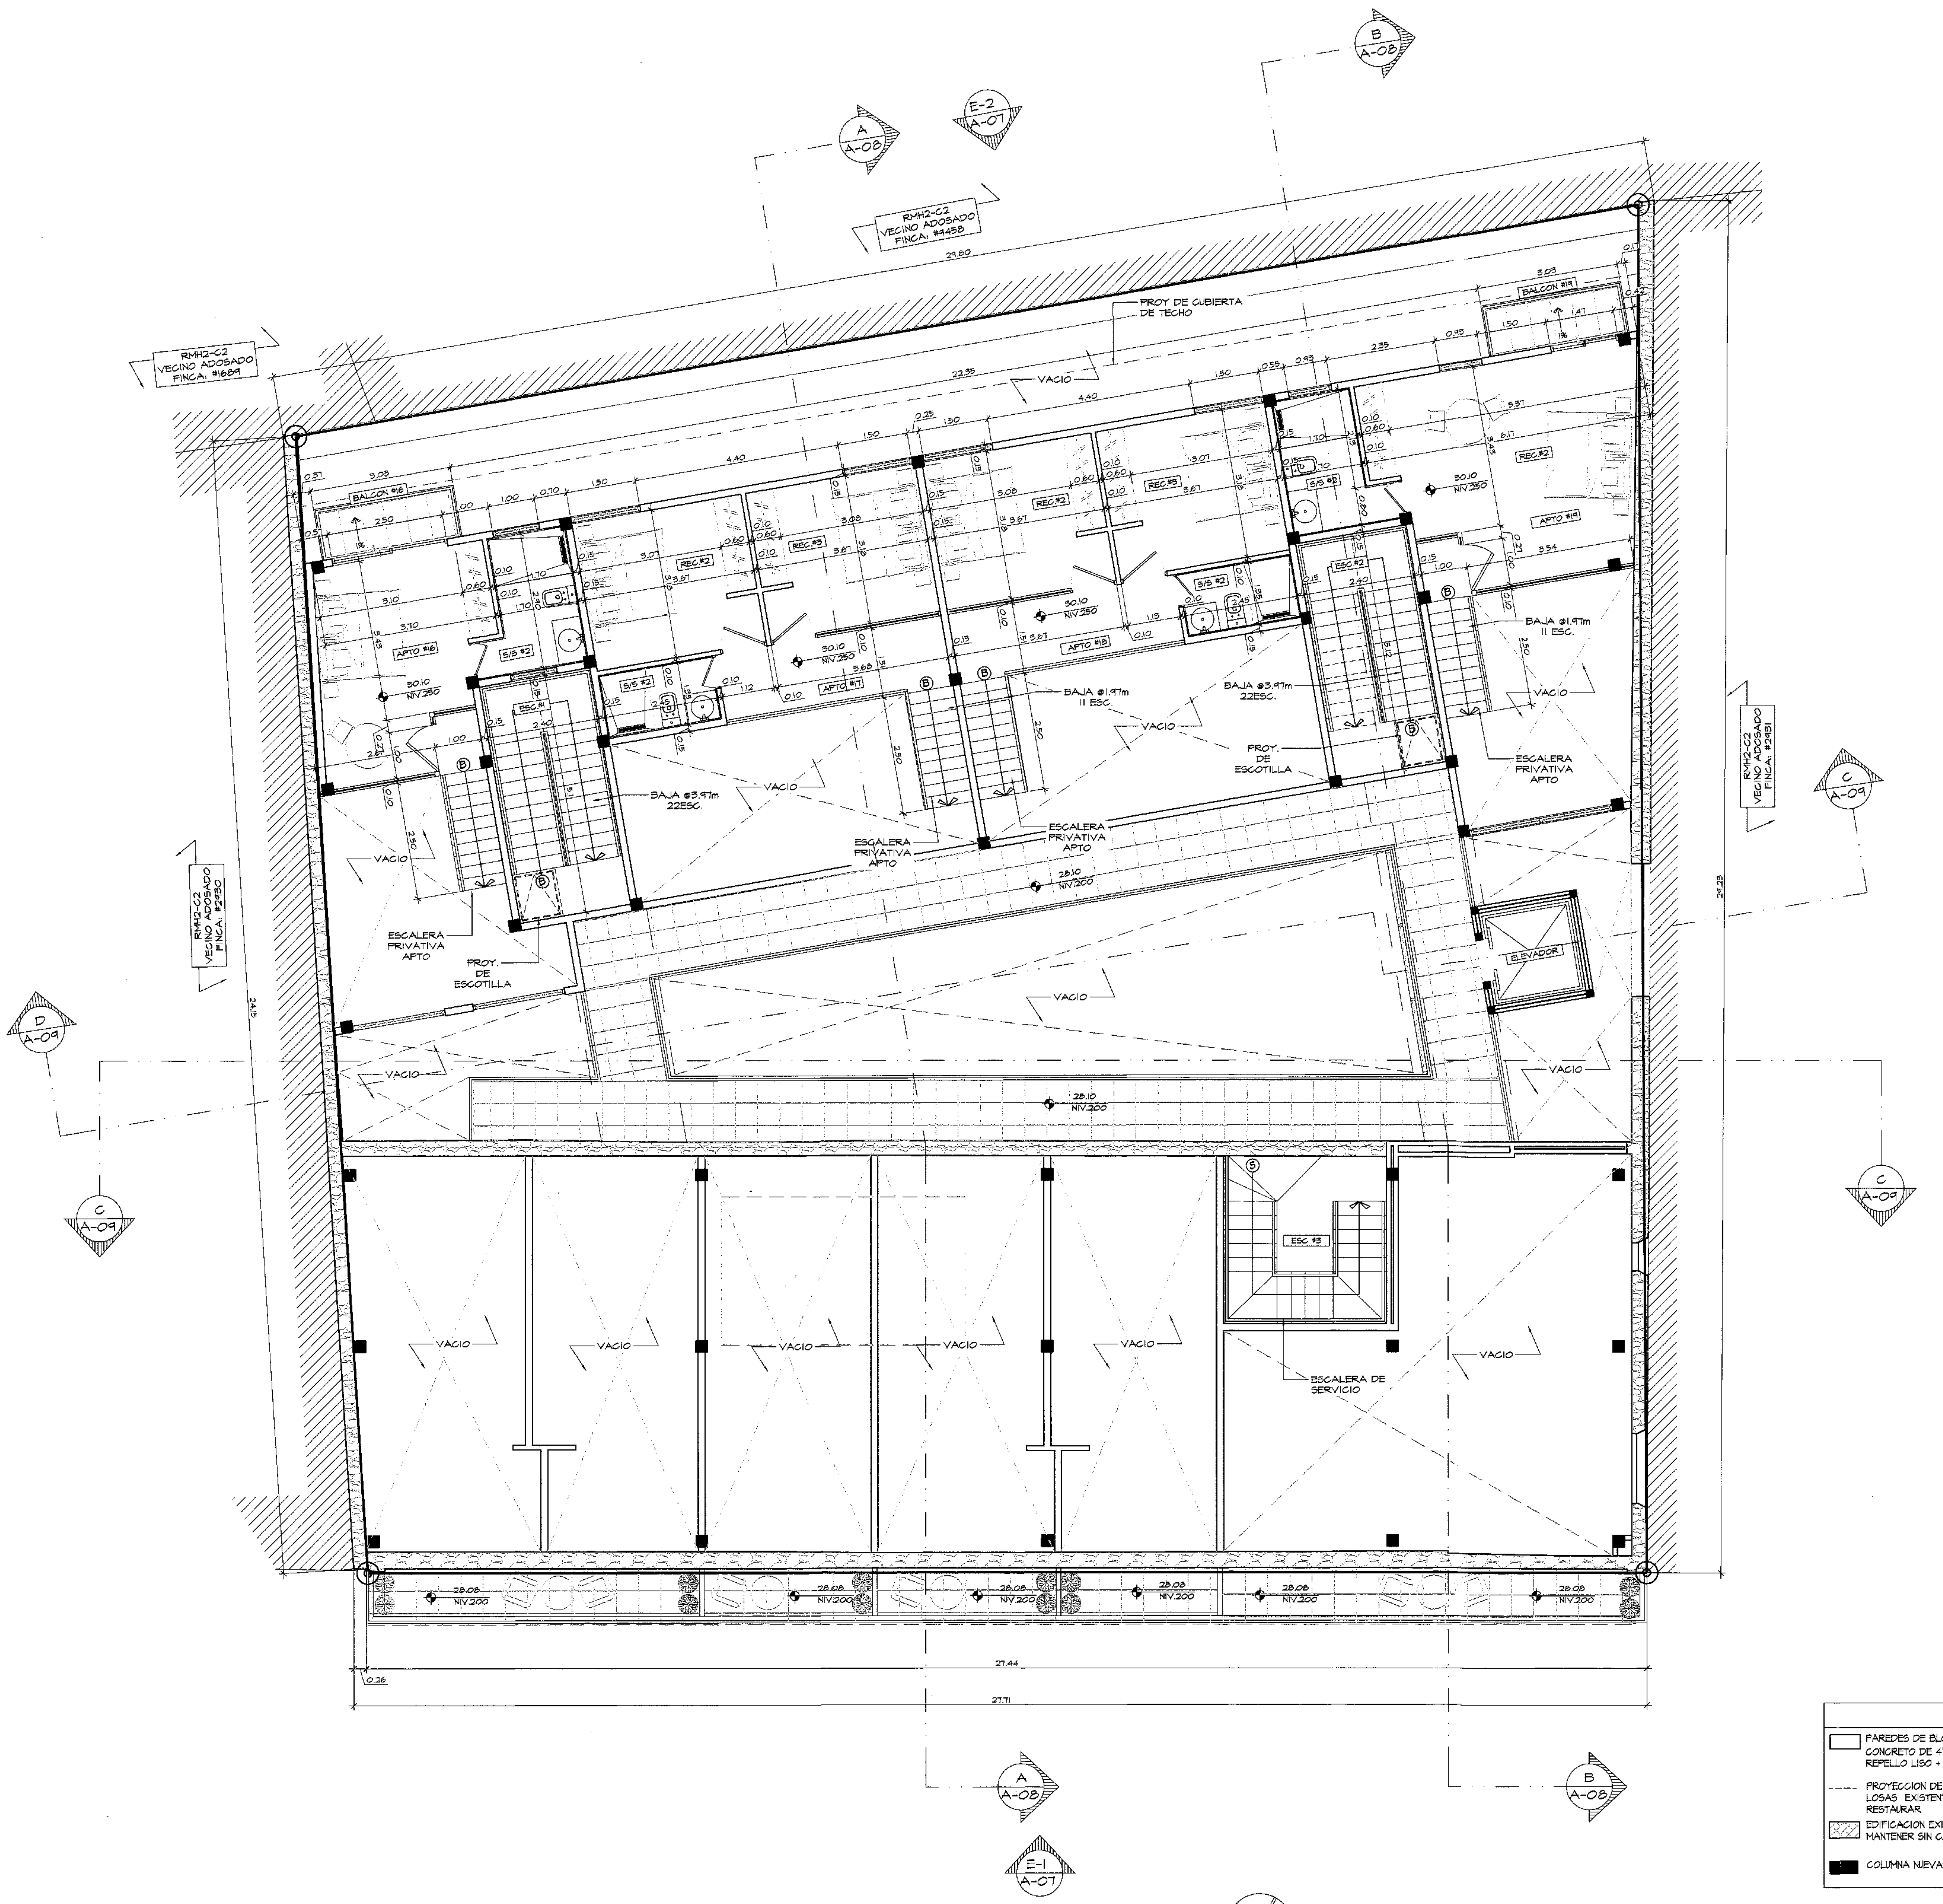

PLANTA ARQUITECTONICA N.250

ANTEPROYECTO

ESC. 1:75

LEYENDA			
▭	PAREDES DE BLOQ'S DE CONCRETO DE 4" Ó 6" Y REPELLO LISO + PINTURA	▨	PAREDES, PISOS Y ESTRUCTURAS EXISTENTES A MANTENER Y RESTAURAR.
- - - -	PROYECCION DE VIGAS DE LOSAS EXISTENTES A RESTAURAR	////	EDIFICIO VECINO ADOSADO.
▨	EDIFICACION EXISTENTES A MANTENER SIN CAMBIOS	▩	LOSA DE CONCRETO NUEVAS
■	COLUMNA NUEVAS A CONSTRUIR	▦	MURO DE CALICANTO EXIST. A MANTENER/RESTAURAR
		#	VÉRTICE DEL POLÍGONO DEL TERRENO

MINISTERIO DE CULTURA
DIRECCIÓN NACIONAL DE PATRIMONIO CULTURAL
Día de hoy 02 de 10 de 2023
Certificamos que esta copia del Plano corresponde a los Planos
Anteproyecto Aprobados
mediante Resolución No. 106-2023 MC/DNPC
Firma del Director

DANIEL YOUNG TORQUEMADA
ARQUITECTO
LICENCIA No: 95-001-038
FIRMA
Ley 15 del 26 de enero de 1959
Junta Técnica de Ingeniería y Arquitectura

El Plano es propiedad intelectual del arquitecto esta prohibida su reproducción total o parcial, y no puede ser alterado o modificado sin su consentimiento previo por escrito.

PROYECTO: "ANTIGUA BAJADA"
PROPIEDAD: Creative Development, Inc.
UBICACION: Calle 12 Este, Casco Antiguo, Corregimiento de San Felipe,
Panamá, Provincia de Panamá

DISEÑO:
Arq. Daniel Young
Torquemada

DESARROLLO:
Ytarquitectos

DIBUJO:
Ytarquitectos

FECHA
Septiembre 2023

Director de obras y construcciones municipales

Rep. Legal
Céd:2-113-694

A-05

05/11

YOUNG
TORQUEMADA
ARQUITECTOS
Tel. (507) 264-0711 (507) 264-2670
info@ytarquitectos.com
www.ytarquitectos.com

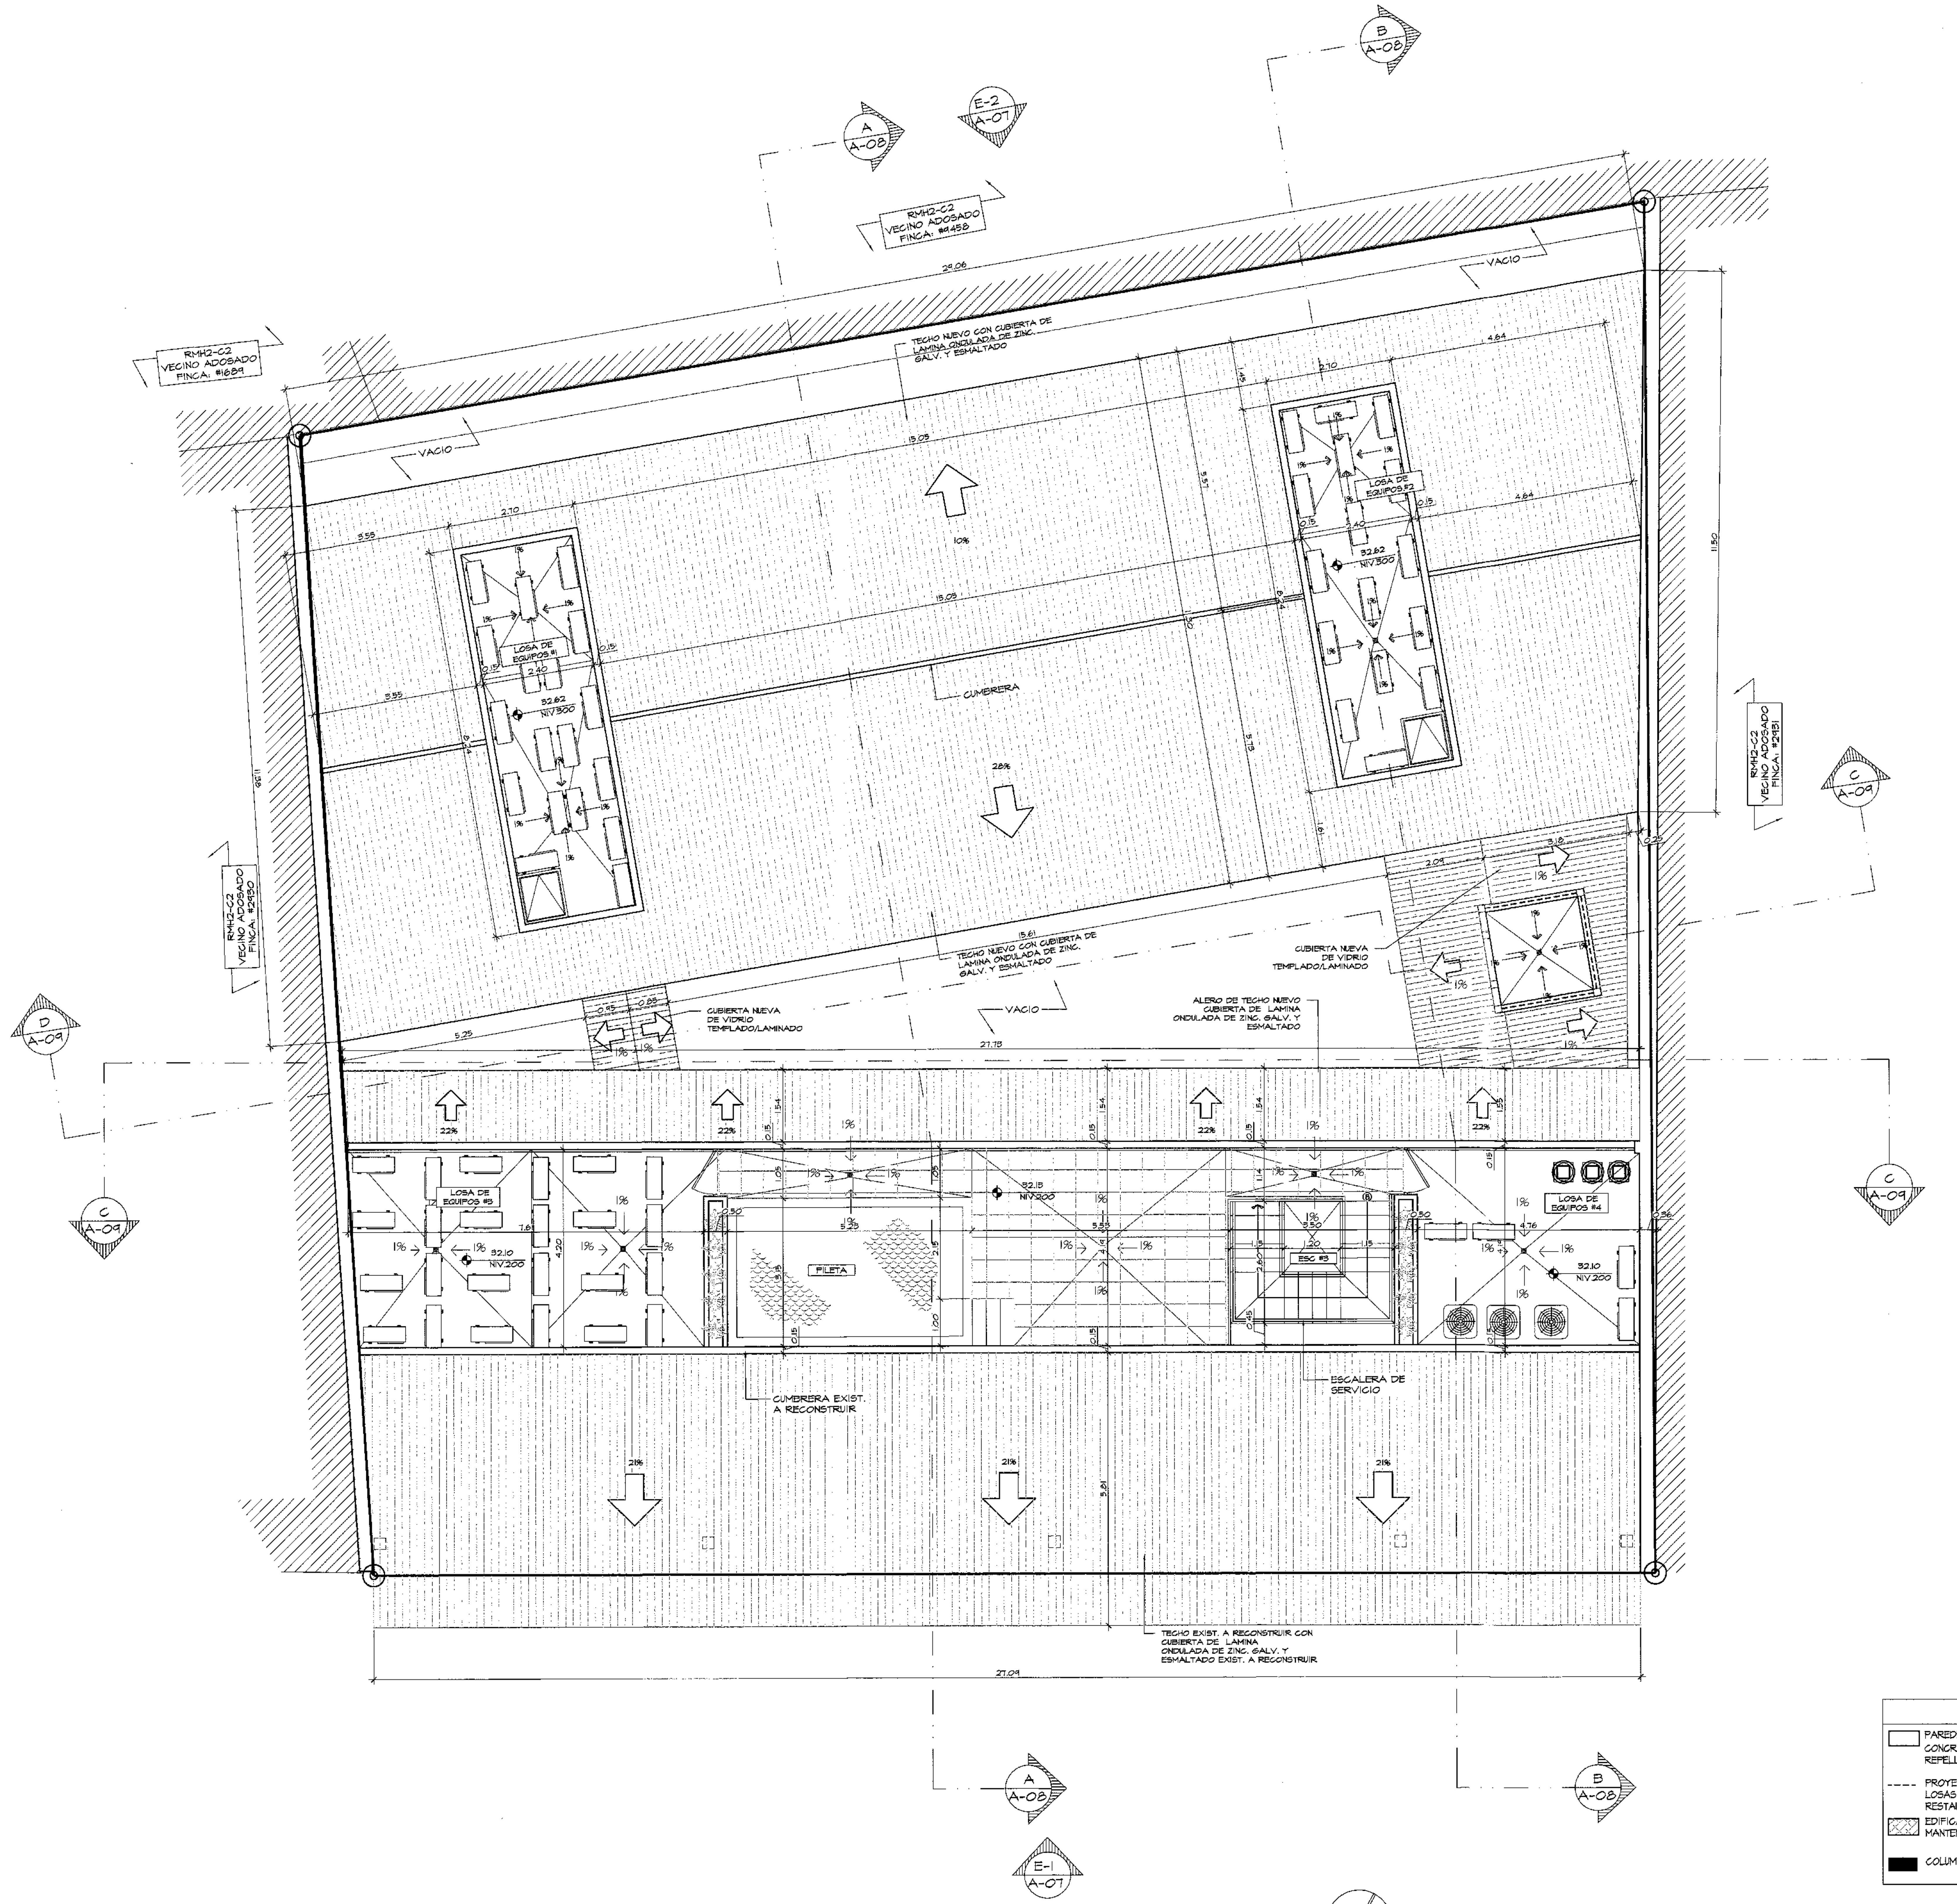

PLANTA ARQUITECTONICA NIVEL300/TECHOS

ANTEPROYECTO

ESC. 1:75

LEYENDA

☐	PAREDES DE BLOQ'S DE CONCRETO DE 4" Ó 6" Y REPELLO LISO + PINTURA	▨	PAREDES, PISOS Y ESTRUCTURAS EXISTENTES A MANTENER Y RESTAURAR.
----	PROYECCION DE VIGAS DE LOSAS EXISTENTES A RESTAURAR	////	EDIFICIO VECINO ADOSADO.
▨	EDIFICACION EXISTENTES A MANTENER SIN CAMBIOS	░	LOSA DE CONCRETO NUEVAS
■	COLUMNA NUEVAS A CONSTRUIR	▨	MURO DE CALICANTO EXIST. A MANTENER/RESTAURAR
		#	VÉRTICE DEL POLÍGONO DEL TERRENO

MINISTERIO DE CULTURA
DIRECCION NACIONAL DE PATRIMONIO CULTURAL
Día de hoy 02 de 10 de 20 23
Certificamos que esta hoja de Plano corresponde a los Planos
Anteproyecto Aprobados
mediante Resolución DNPC-MiCULTURA-YY3 MiCDNPC
Firma del Director

DANIEL YOUNG TORQUEMADA
ARQUITECTO
LICENCIA No. 95-001-038
FIRMA
Ley 15 del 26 de enero de 1959
Junta Técnica de Ingeniería y Arquitectura

El Plano es propiedad intelectual del arquitecto esta prohibida su reproducción total o parcial, y no puede ser alterado o modificado sin su consentimiento previo por escrito.

PROYECTO: "ANTIGUA BAJADA"
PROPIEDAD: Creative Development, Inc.
UBICACION: Calle 12 Este, Casco Antiguo, Corregimiento de San Felipe, Panamá, Provincia de Panamá

DISEÑO: Arq. Daniel Young Torquemada
DESARROLLO: Ytarquitectos
DIBUJO: Ytarquitectos
FECHA Septiembre 2023

A-06
06/11

Director de obras y construcciones municipales

Rep. Legal
Céd:2-113-694

YOUNG
TORQUEMADA
ARQUITECTOS
Tel. (507) 264-0711 (507) 264-2670
info@ytarquitectos.com
www.ytarquitectos.com

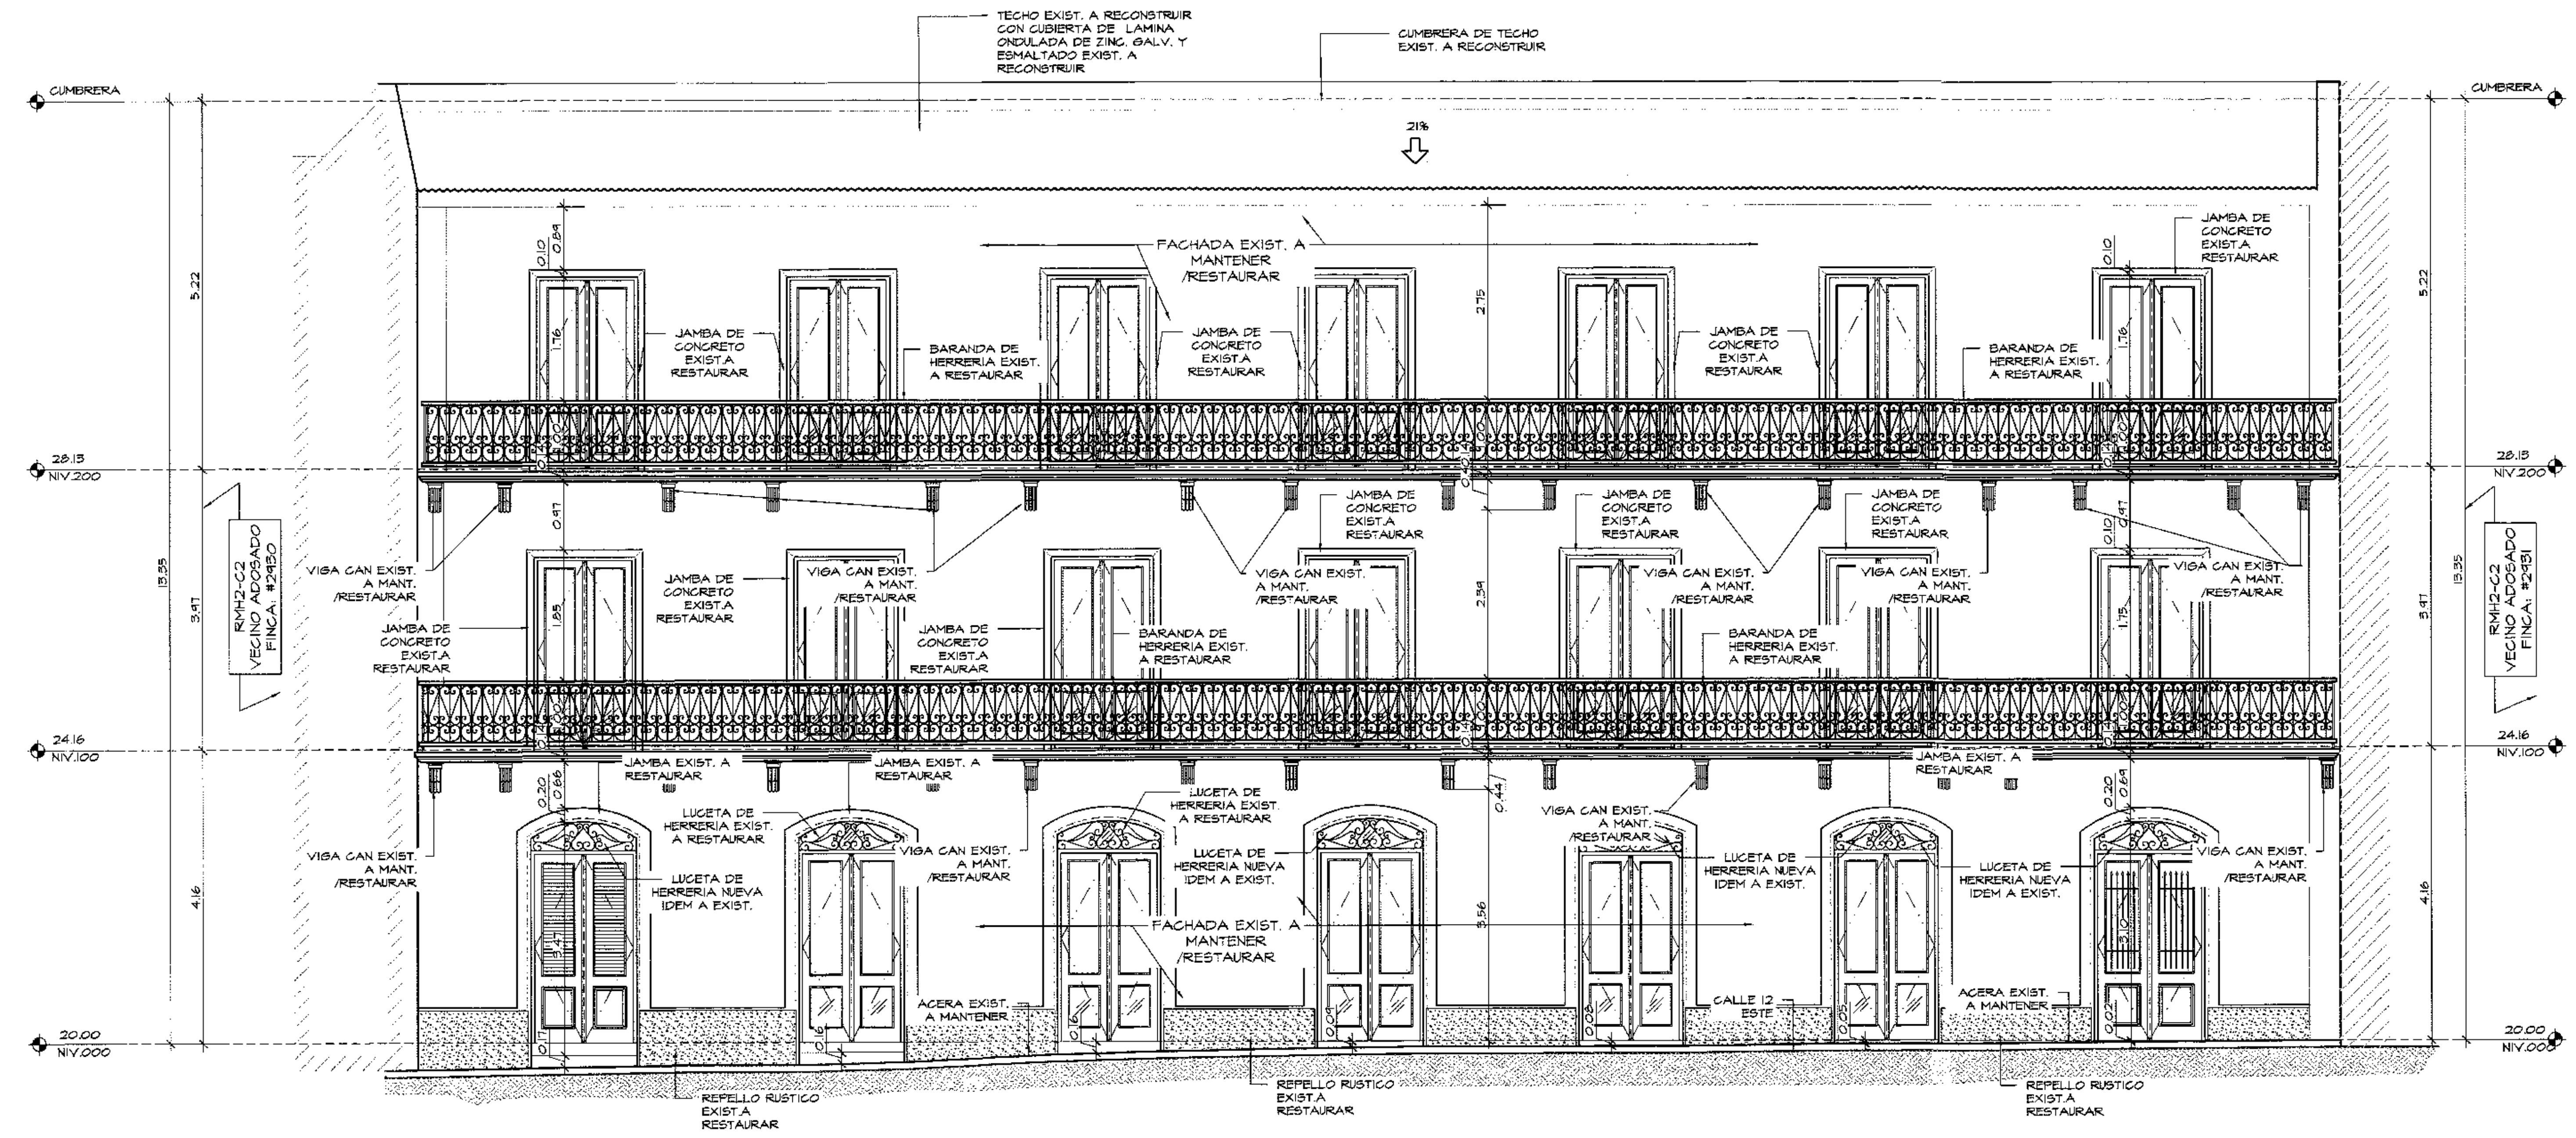
TECHO EXIST. A RECONSTRUIR CON CUBIERTA DE LAMINA ONDULADA DE ZINC. GALV. Y ESMALTADO EXIST. A RECONSTRUIR
CUMBRERA DE TECHO EXIST. A RECONSTRUIR
CUMBRERA
21%
FACHADA EXIST. A MANTENER /RESTAURAR
JAMBA DE CONCRETO EXIST.A RESTAURAR
BARANDA DE HERRERIA EXIST. A RESTAURAR
VIGA CAN EXIST. A MANT. /RESTAURAR
JAMBA EXIST. A RESTAURAR
LUCETA DE HERRERIA EXIST. A RESTAURAR
LUCETA DE HERRERIA NUEVA IDEM A EXIST.
ACERA EXIST. A MANTENER
CALLE 12 ESTE
REPELLO RUSTICO EXIST.A RESTAURAR
RMH2-C2 VECINO ADOSADO FINCA: #2930
RMH2-C2 VECINO ADOSADO FINCA: #2931
28.13 NIV.200
24.16 NIV.100
20.00 NIV.000
5.22
3.97
4.16
13.35

ELEVACION FRONTAL

RESTAURADA ESC. 1:75

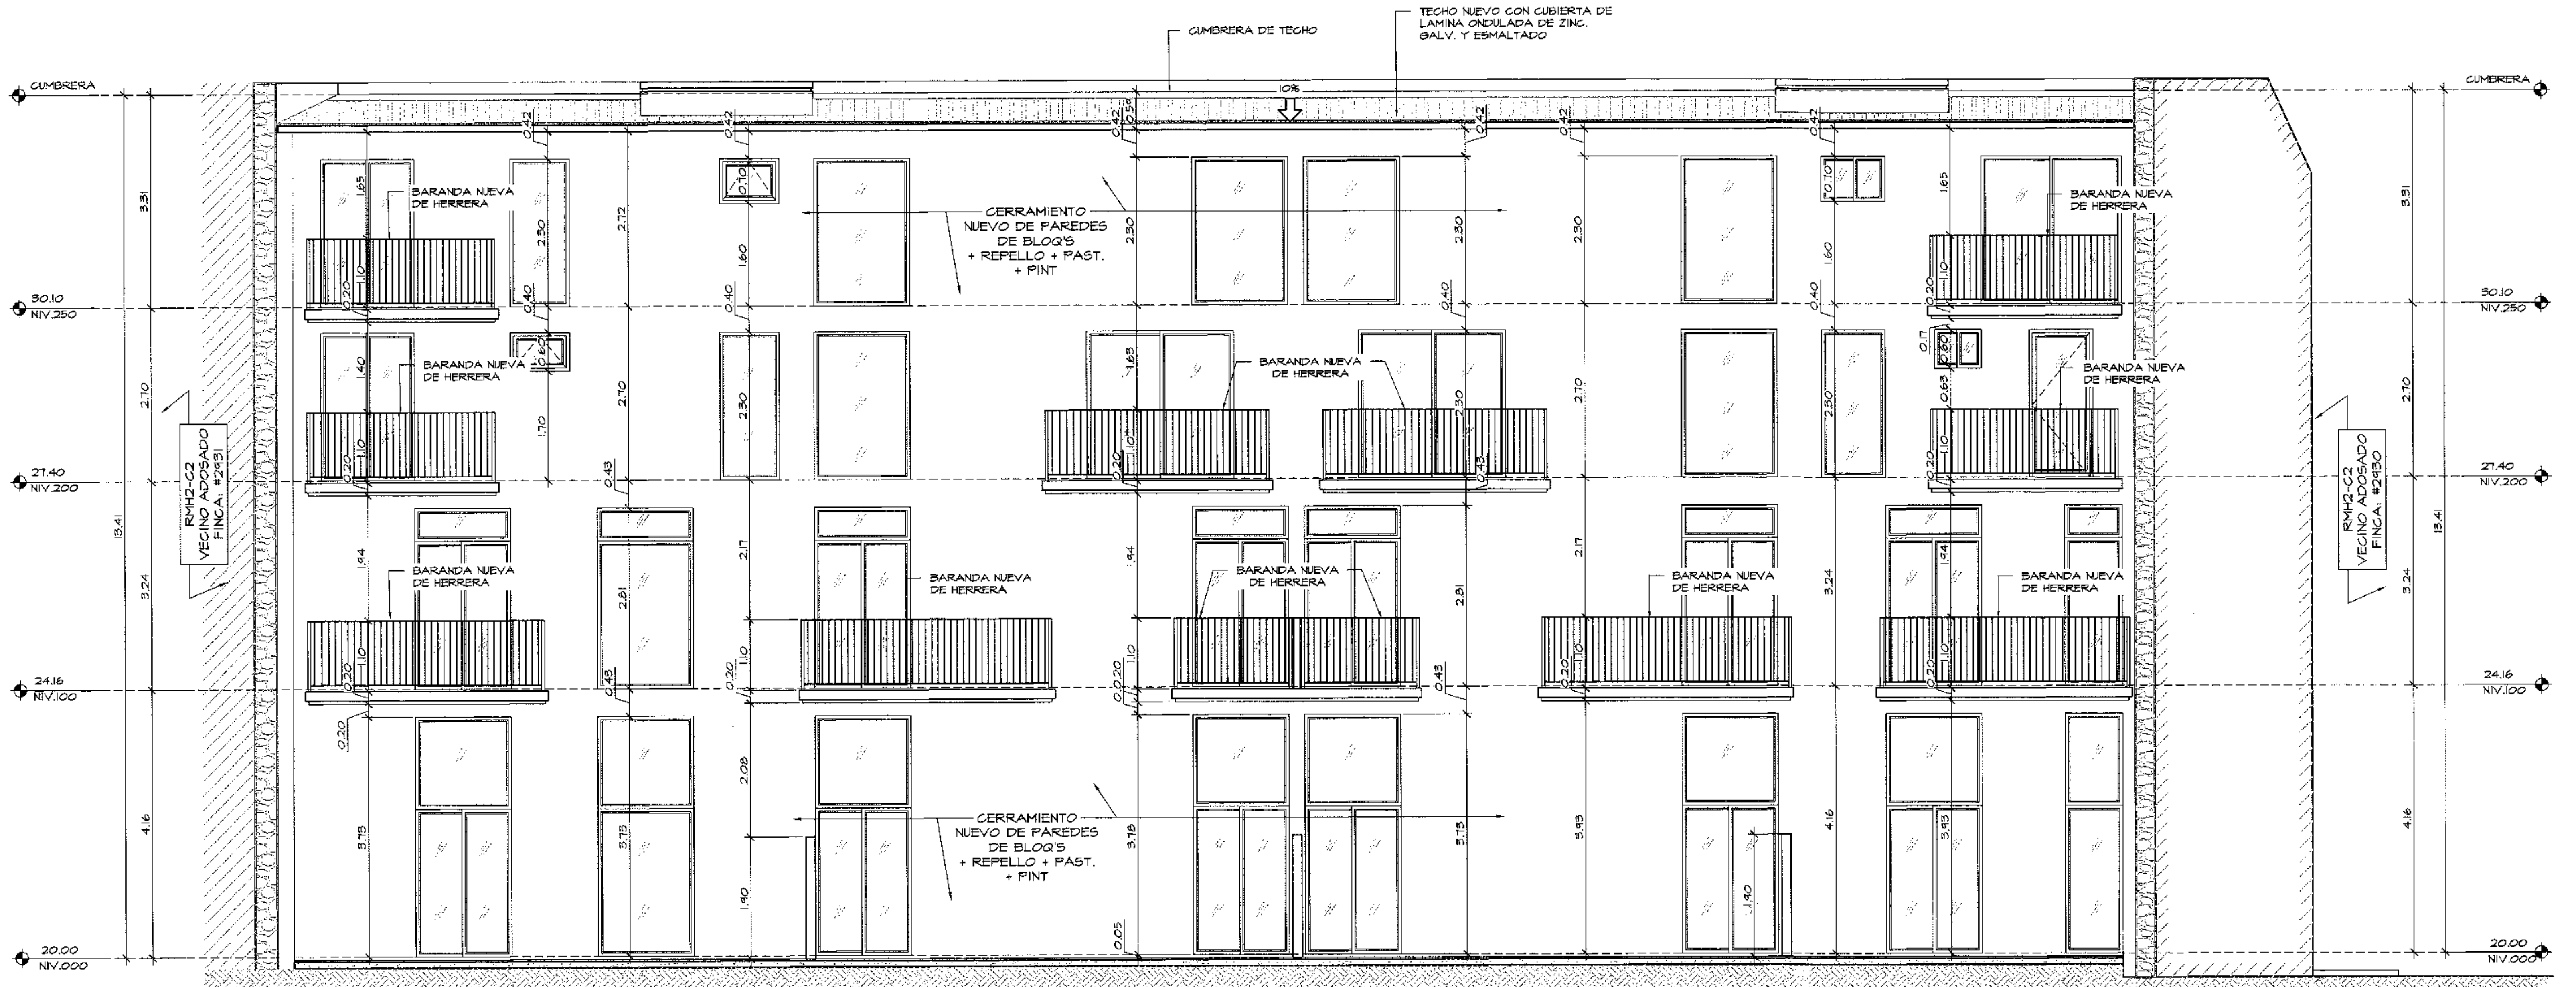
CUMBRERA DE TECHO
TECHO NUEVO CON CUBIERTA DE LAMINA ONDULADA DE ZINC. GALV. Y ESMALTADO
10%
CUMBRERA
BARANDA NUEVA DE HERRERA
CERRAMIENTO NUEVO DE PAREDES DE BLOQ'S + REPELLO + PAST. + PINT
RMH2-C2 VECINO ADOSADO FINCA: #2931
RMH2-C2 VECINO ADOSADO FINCA: #2930
30.10 NIV.250
27.40 NIV.200
24.16 NIV.100
20.00 NIV.000
3.31
2.70
3.24
4.16
13.41

ELEVACION POSTERIOR (INTERNA)

ANTEPROYECTO ESC. 1:75

DANIEL YOUNG TORQUEMADA
ARQUITECTO
LICENCIA No. 95-001-038
FIRMA
Ley 15 del 26 de enero de 1959
Junta Técnica de Ingeniería y Arquitectura

MINISTERIO DE CULTURA
DIRECCIÓN NACIONAL DE PATRIMONIO CULTURAL
Panamá, de hoy 06 de 10 de 2023
Certificamos que esta hoja de Plano corresponde a los Planos aprobados
Anteproyecto
mediante Resolución No. 160 [illegible]
Firma del Director

El Plano es propiedad intelectual del arquitecto esta prohibida su reproducción total o parcial, y no puede ser alterado o modificado sin su consentimiento previo por escrito.

PROYECTO: "ANTIGUA BAJADA"

PROPIEDAD:Creative Development, Inc.
UBICACION: Calle 12 Este, Casco Antiguo,Corregimiento de San Felipe, Panamá, Provincia de Panamá

Director de obras y construcciones municipales

Rep. Legal
Céd:2-113-694

DISEÑO:
Arq. Daniel Young Torquemada

DESARROLLO:
Ytarquitectos

DIBUJO:
Ytarquitectos

FECHA
Septiembre 2023

A-07 | 07/ 11

YOUNG
TORQUEMADA
ARQUITECTOS

Tel. (507) 264-0711 (507) 264-2670
info@ytarquitectos.com
www.ytarquitectos.com